


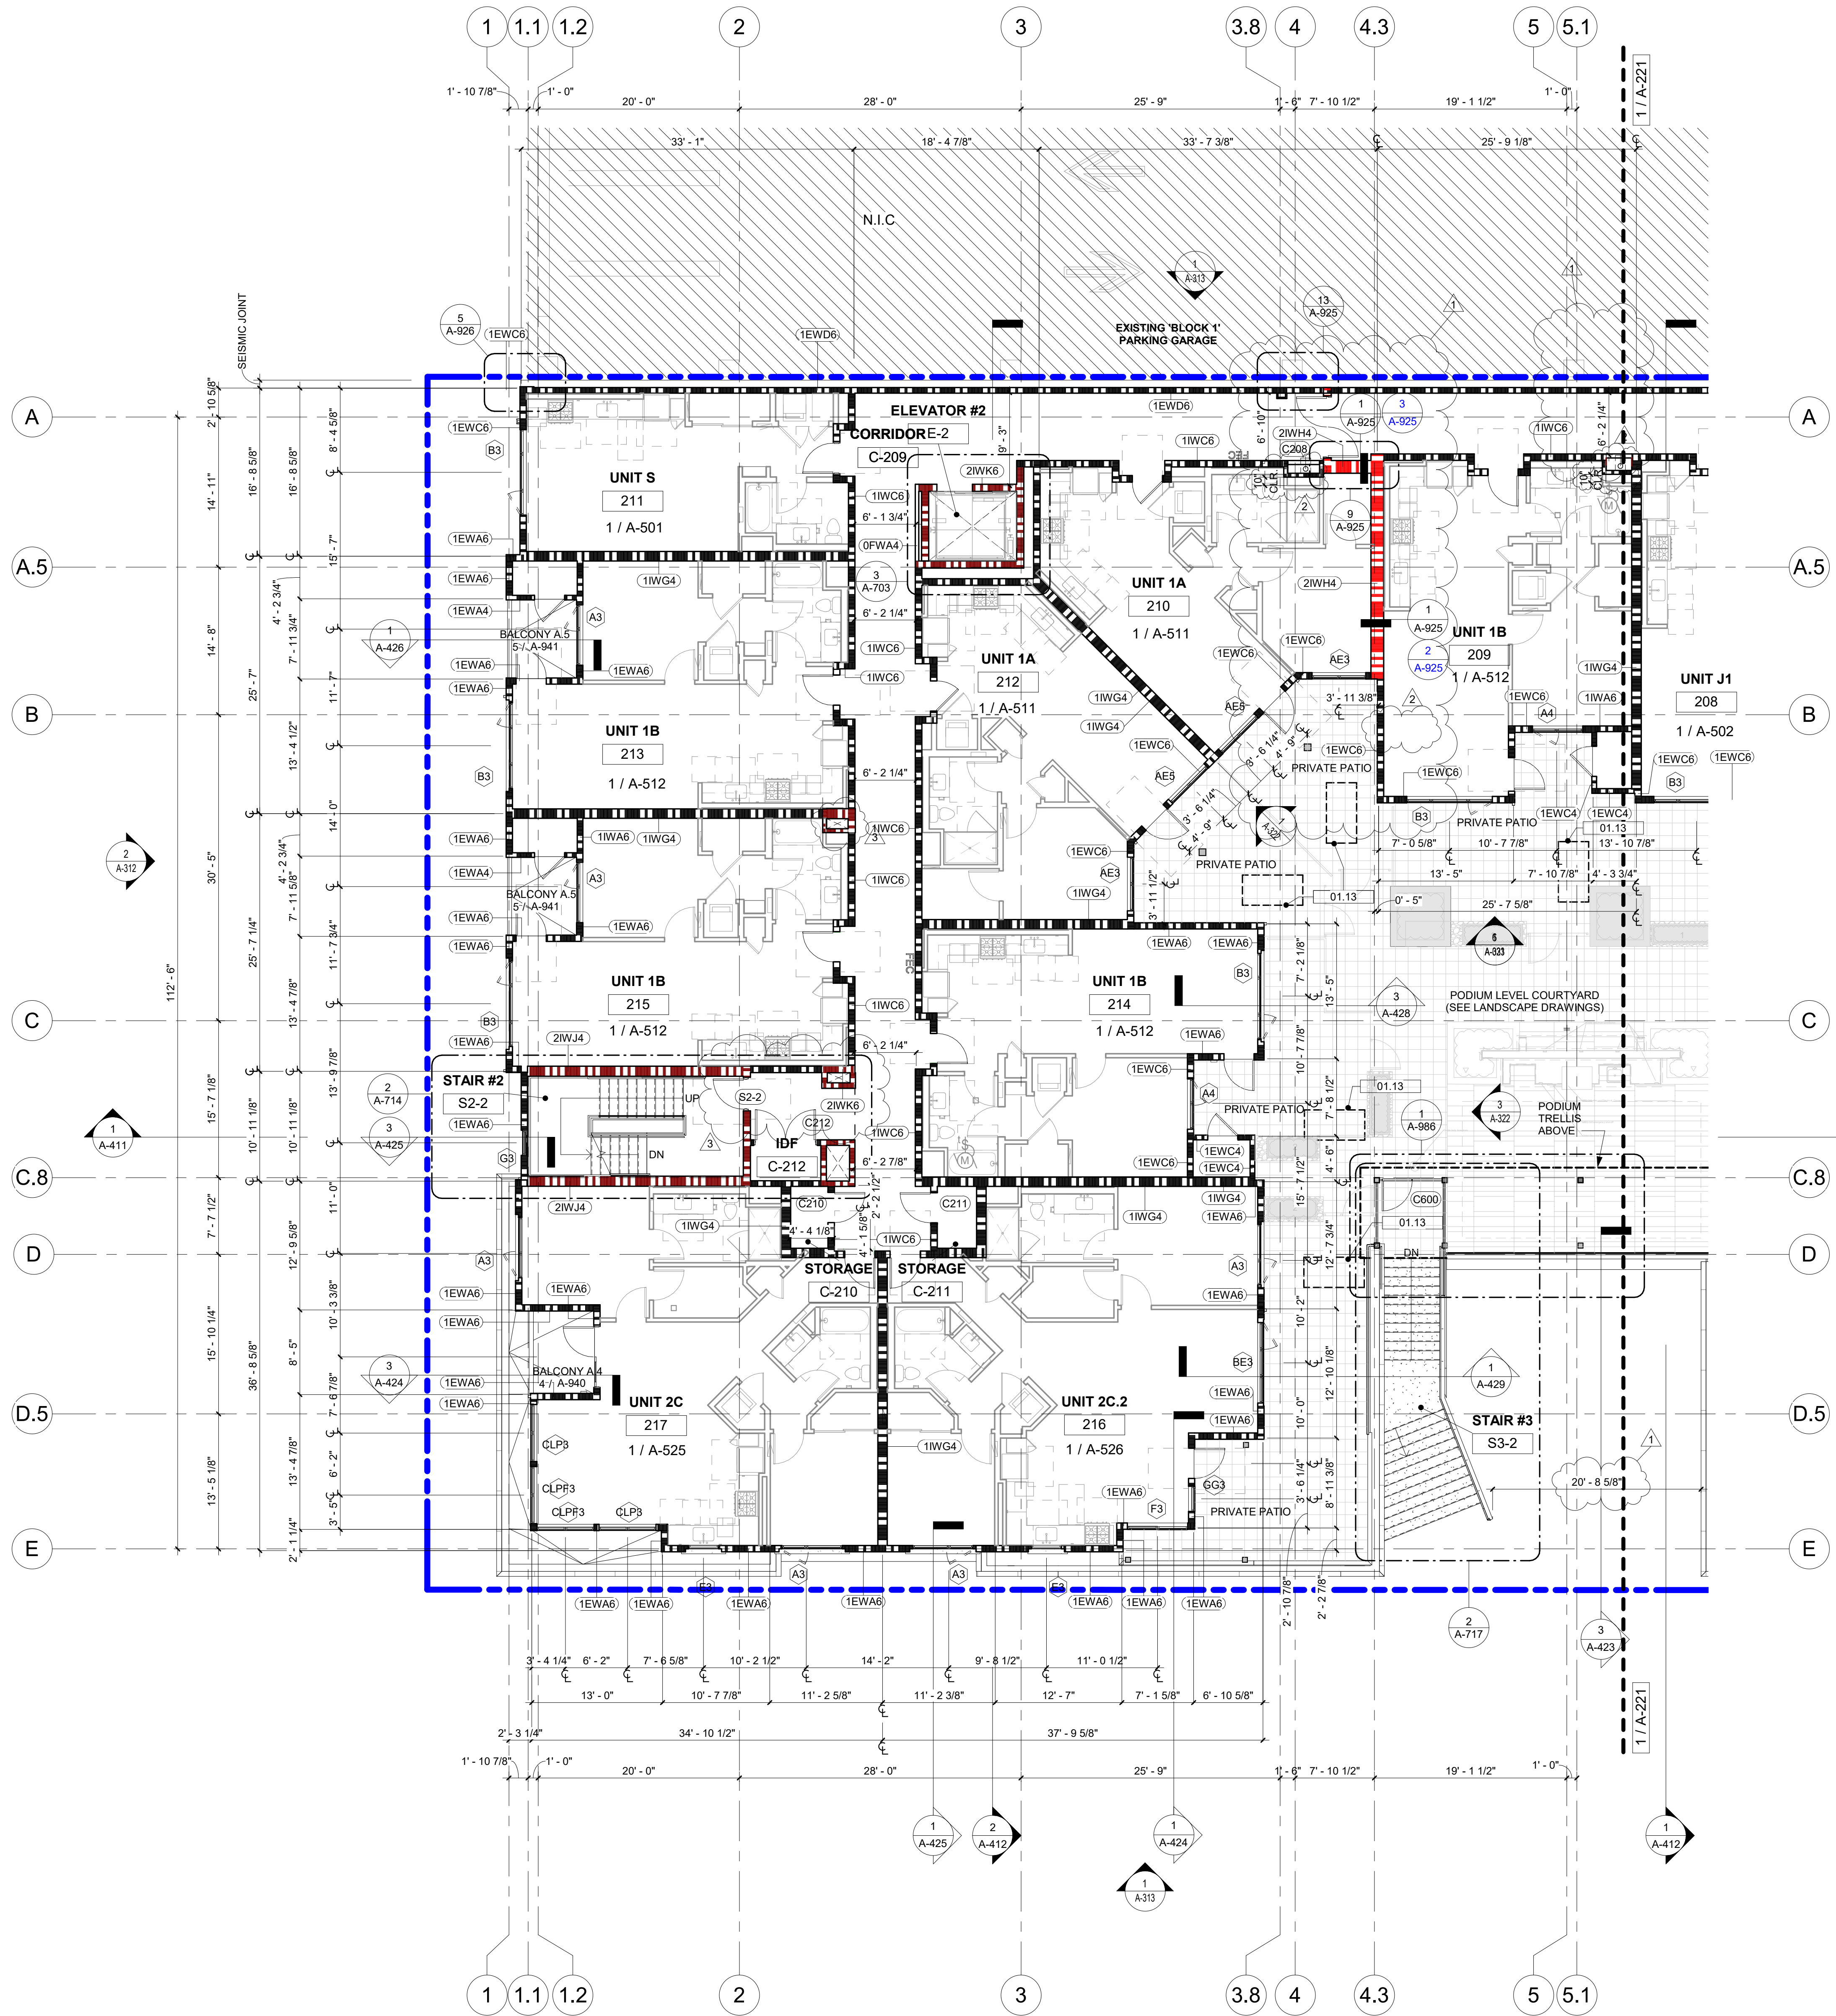

PLAN GENERAL NOTES

- ALL EXTERIOR WALLS AT TYPE VA CONSTRUCTION ARE 1-HR RATED AND MINIMUM 6" WIDE. SEE DETAILS ON SHEET A-912 FOR EXTERIOR WALL TO FLOOR ASSEMBLIES.
- SEE ENLARGED RESIDENTIAL UNIT AND COMMON AREAS PLANS IN SERIES A-500 SHEETS FOR DIMENSIONAL LAYOUT WITHIN EACH UNIT. IF ANY DISCREPANCIES EXIST BETWEEN THE UNIT PLANS & BUILDING PLANS, THE CONTRACTOR SHALL CONSULT THE ARCHITECT BEFORE PROCEEDING WITH THE WORK.
- BUILDING EXTERIOR, CORRIDOR PARTY WALL TYPES ARE NOTED ON BUILDING FLOOR PLANS. SEE ENLARGED PLANS IN SERIES A-500 & A-700 DRAWINGS FOR WALL DESIGNATIONS INTERNAL TO THE UNITS AND COMMON AREA. FOR COMMON AREA INTERIOR DESIGN REFER TO THE ID DRAWINGS.
- ALL DIMENSIONS ARE FACE OF STUD (FOS) UNLESS OTHERWISE NOTED. IF ANY DISCREPANCIES EXIST BETWEEN DRAWING & DIMENSIONS, DIMENSIONS TAKE PRECEDENCE.
- ALL FIRE WALLS, FIRE BARRIERS, FIRE PARTITIONS SMOKE BARRIERS, SMOKE PARTITIONS OR ANY OTHER WALL REQUIRED TO HAVE PROTECTED OPENINGS OR PENETRATIONS SHALL BE EFFECTIVELY AND PERMANENTLY IDENTIFIED WITH SIGNS OR STENCILING AS REQUIRED BY CBC SECTION 703.6.
- ALL COMMON AREA DOORS, INCLUDING CORRIDOR, BUILDING ENTRY, UTILITY ROOM DOORS ARE NOTED ON THE BUILDING PLANS IN THE SERIES A-200 SHEETS.
- UNIT ENTRY DOORS AND DOORS INTERNAL TO THE UNITS ARE NOTED ON THE ENLARGED UNIT PLANS IN THE A-500 SERIES SHEETS.
- SMOKE ALARMS SHALL BE INTERCONNECTED IN SUCH A MANNER THAT THE ACTIVATION OF ONE ALARM WILL ACTIVATE ALL ALARMS IN THE INDIVIDUAL UNIT. THE ALARM SHALL BE CLEARLY AUDIBLE IN ALL BEDROOMS OVER BACKGROUND NOISE LEVELS WITH ALL INTERVENING DOORS CLOSED - PER CBC SECTION 907.2.10.3.
- SEE SHEETS A900-A920 FOR CONSTRUCTION ASSEMBLIES. ASSEMBLIES ARE INDICATED ON THE PLANS AND SECTIONS.
- FIRE EXTINGUISHERS SHALL BE INSTALLED IN RECESSED CABINETS WHERE SHOWN OR AS REQUIRED BY THE BUILDING DEPARTMENT. THE MINIMUM RATING OF FIRE EXTINGUISHER SHALL BE 2A10BC.
- ROOM AND UNIT PLAN NUMBERING IS FOR CONSTRUCTION PURPOSES ONLY. VERIFY EXACT NUMBERS WITH OWNER PRIOR TO FABRICATING ROOM IDENTIFICATION SIGNAGE.
- VERIFY LOCATION OF KNOX BOX WITH FIRE DEPARTMENT PRIOR TO INSTALLING. SEE ELECTRICAL AND LOW VOLTAGE DRAWINGS FOR BUILDING SECURITY SYSTEMS, SUCH AS CARD READERS AND CALL BOXES.
- SEE SHEET A-040THRU A-046 FOR ACCESSIBILITY STANDARDS AND DETAILS APPLICABLE TO THE PROJECT
- THE SUFFIX "M" AFTER A UNIT TYPE DESIGNATION ON LEVEL 1 INDICATES FRAMING WITH METAL STUDS



PLAN LEGEND

- FINISH SURFACE ELEVATION RELATIVE TO DATUM
- 1/4" PER 12" MAX, 1/8" PER 12" MIN FLOOR SLOPE. SLOPE TO DRAIN OR GUTTER
- FLOOR DRAIN, SEE PLUMBING DRAWINGS
- DETECTABLE WARNING, SEE 17A-40
- FIRE EXTINGUISHER CABINET RECESSED
- STAND PIPE
- KNOX BOX, FINAL LOCATIONS TO BE APPROVED BY OFD

WALL PATTERNS LEGEND

- STRUCTURAL CONCRETE WALL, S.S.D.
- 3 HOUR RATED STRUCT. CONCRETE WALL, SSD.
- STRUCTURAL CMU WALL, SSD
- 2 HOUR RATED FIRE WALL, TYP.
- 2 HOUR RATED WALL, TYP.
- 1 HOUR RATED WALL, TYP.
- STUD PARTITION SEE WALL CALL-OUTS FOR FRAMING MATERIAL

KEYNOTES

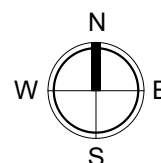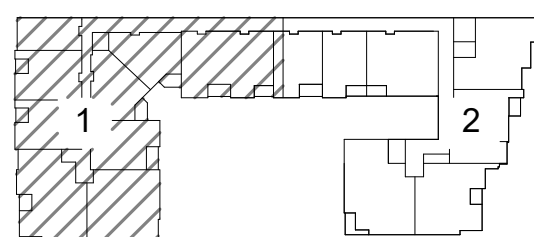

Architecture
Planning
Urban Design

1970 Broadway, Suite 500
Oakland, California 94612
(510) 451-2850

SARES REGIS

CITYLINE

Cityline Sunnyvale F-1 Development

333 West Iowa Avenue, Sunnyvale, CA 94086

STC Venture, LLC

901 Mariners Island Boulevard, San Mateo, CA 94404

REV	DESCRIPTION	DATE
50%	DESIGN DEVELOPMENT	09/05/2018
100%	DESIGN DEVELOPMENT	10/18/2018
50%	CONSTRUCTION DOCUMENTS	02/20/2019
PERMIT SET		04/03/2019
1	PERMIT RESUBMITTAL #1	06/13/2019
2	PERMIT RESUBMITTAL #2	08/09/2019
3	PERMIT RESUBMITTAL #3	09/20/2019



Sheet Title:

BUILDING PLAN
LEVEL 2
SEGMENT 1

Job No: 16039
Date: 09/20/2019
Scale: As indicated

Sheet No:

A-220