



STUDIO
T SQUARE

: Architecture
: Planning
: Urban Design

: 1970 Broadway, Suite 500
: Oakland, California 94612
: (510) 451 - 2850

THIS DOCUMENT CONTAINS INFORMATION
PROPRIETARY TO STUDIO T-SQ, INC. AND IS
FURNISHED IN CONFIDENCE FOR THE LIMITED
PURPOSE OF EVALUATION OR REVIEW. THIS
DOCUMENT OR ITS CONTENTS MAY NOT BE USED
FOR ANY OTHER PURPOSE AND MAY NOT BE
REPRODUCED OR DISCLOSED TO OTHERS
WITHOUT THE PRIOR WRITTEN CONSENT OF
STUDIO T-SQ, INC. ALL RIGHTS
RESERVED. COPYRIGHT 2019.

SARES REGIS

CITYLINE

Cityline Sunnyvale F-1 Development

333 West Iowa Avenue, Sunnyvale, CA 94086

STC Venture, LLC

901 Mariners Island Boulevard, San Mateo, CA 94404

REV	DESCRIPTION	DATE
50%	DESIGN DEVELOPMENT	09/05/2018
100%	DESIGN DEVELOPMENT	10/18/2018
50%	CONSTRUCTION DOCUMENTS	02/20/2019
	PERMIT SET	04/03/2019
1	PERMIT RESUBMITTAL #1	06/13/2019




Sheet Title:

**BUILDING
ELEVATION -
NORTH**

Job No: 16039
Date: 09/20/2019
Scale: As indicated

Sheet No:

A-313

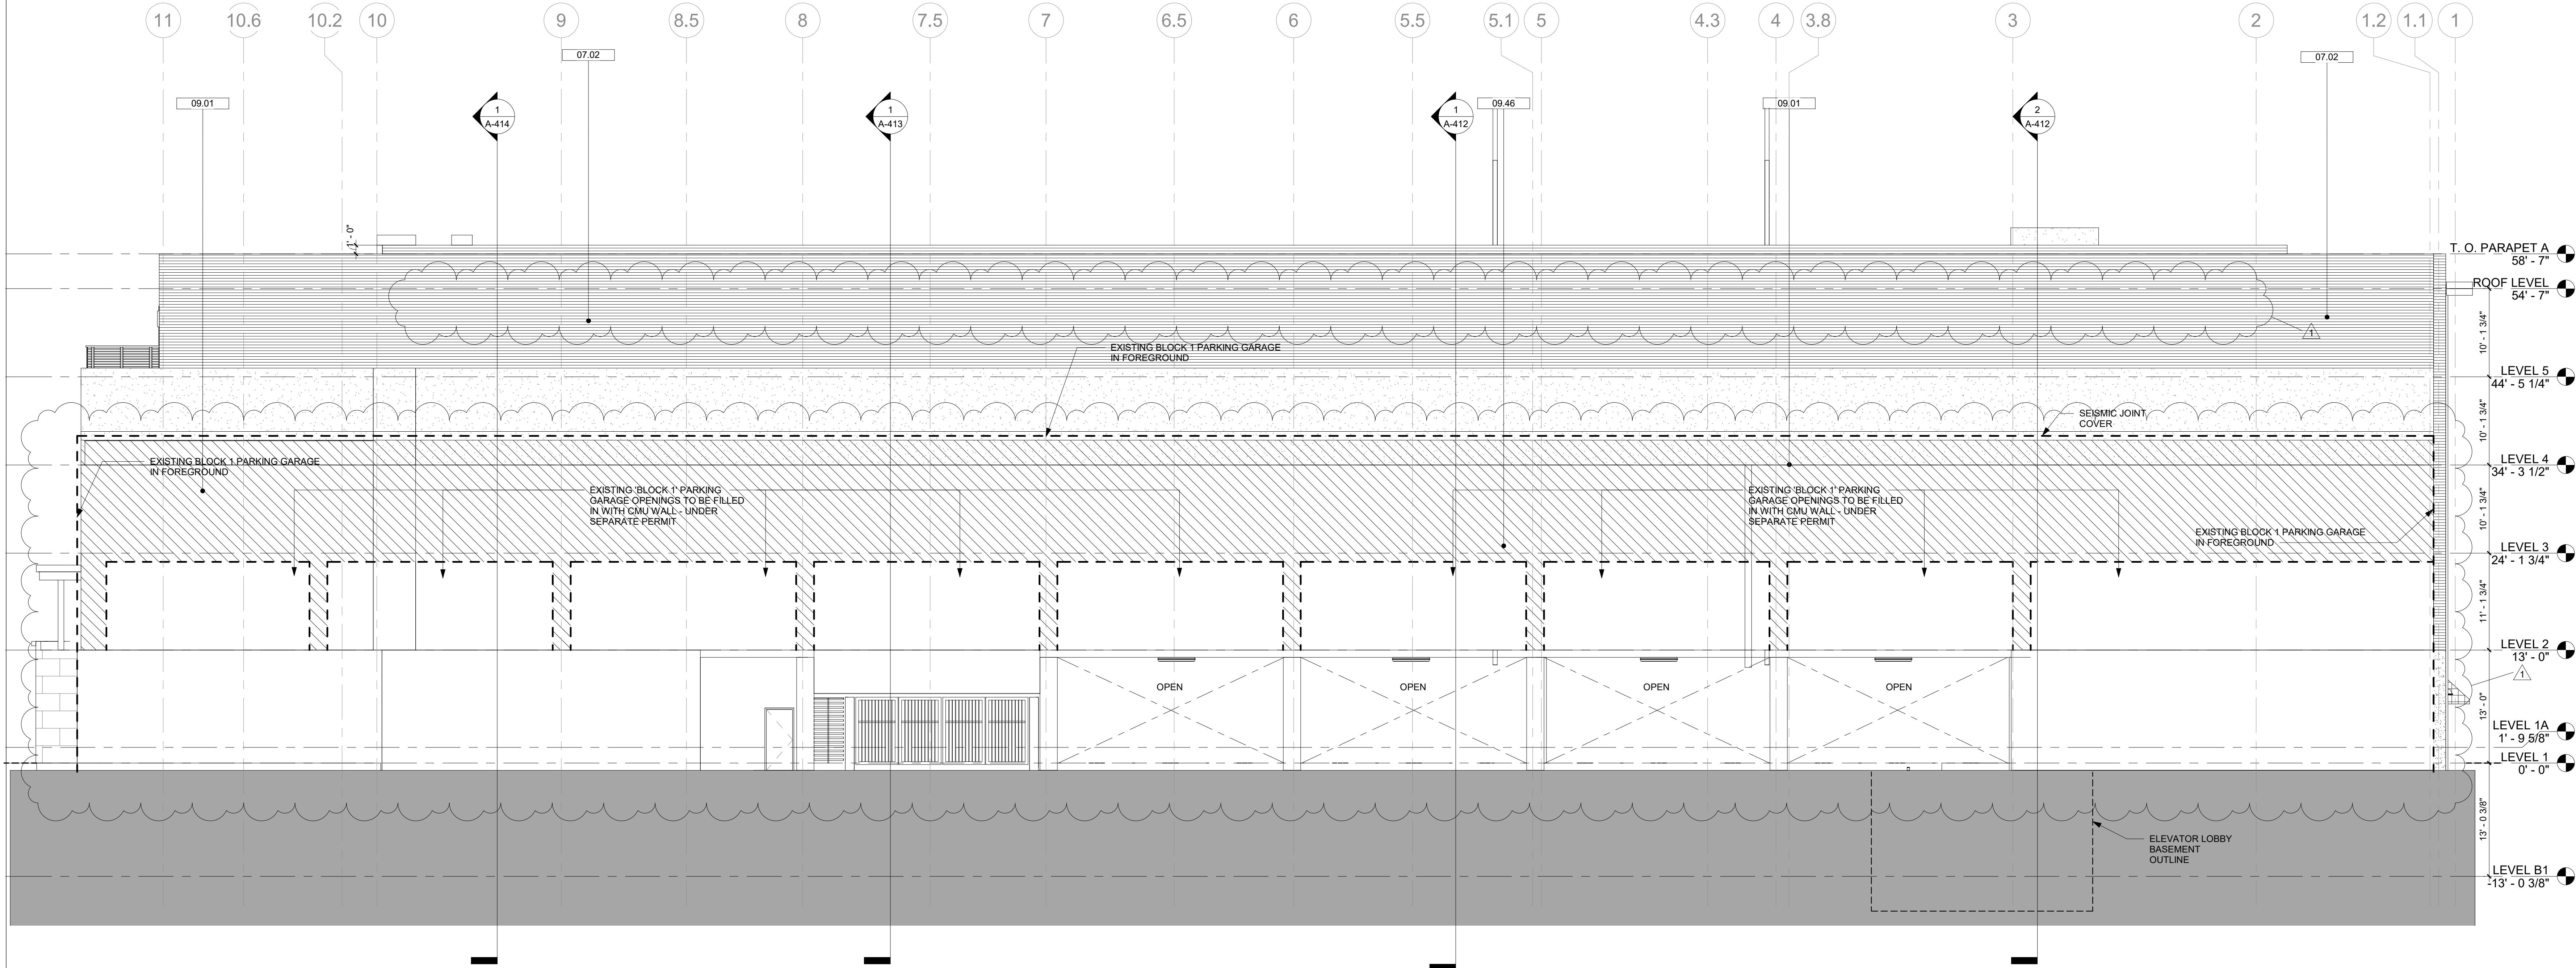

BUILDING ELEVATION - NORTH


1/8" = 1'-0"

1

- ALL VERTICAL PLATE HEIGHTS SHOWN ARE FROM THE INTERIOR TOP OF STRUCTURAL SHEATHING AT THE WOOD FRAMED UPPER FLOORS IN THE TYPE VA CONSTRUCTION OR FINISH FLOOR/SLAB AT THE INTERIOR OF THE TYPE IA CONSTRUCTION.
- COORDINATE LOCATIONS AND QUANTITIES OF EXHUAUST VENT CAPS AND INTAKE AIR LOUVERS WITH MECHANICAL DRAWINGS.
- BUILDING ADDRESS NUMBER SIGN SHALL CONTRAST WITH ITS BACKGROUND.
- HORIZONTAL & VERTICAL CONTROL JOINTS IN EXTERIOR CEMENT PLASTER. LOCATE WHERE INDICATED ON ELEVATIONS OR INSTALL TO SEGREGATE AREAS NOT EXCEEDING MORE THAN 144 SQ. FT. ON WALLS & NOT MORE THAN 100 SQ. FT. ON HORIZONTAL APPLICATIONS. DISTANCE BETWEEN JOINTS SHALL NOT EXCEED 18 FEET IN EITHER DIRECTION OR A LENGTH-TO-WIDTH RATIO OF 2.5 TO 1. HORIZONTAL JOINTS SHALL WRAP OUTSIDE CORNERS AND RETURN TO THE NEAREST INSIDE CORNER ALONG WALLS THAT RETURN TO A SURFACE BEYOND. SEE DETAILS ON SHEET A-975.
- PAINT METAL REVEALS, CONTROL, EXPANSION JOINTS AND PARAPET COPING TO MATCH COLOR OF ADJACENT WALLS.
- PROVIDE FLASHING FOR ALL ITEMS PENETRATING EXTERIOR WALL CONSTRUCTION PER DETAILS; SUCH AS WINDOWS, DOORS, MECHANICAL VENTS, ETC.
- FOR TYPICAL CEMENT PLASTER ASSEMBLY DETAILS, JOINTS, CORNER TRANSITIONS, TRIMS AND PENETRATIONS: SEE SHEET A-975. EXTERIOR WALL ASSEMBLY SHALL COMPLY WITH THE REQUIREMENTS OF CBC 2603.5 & COMPLY WITH ACCEPTANCE CRITERIA OF NFPA 285.
- ALL EXPOSED GSM FLASHING, COPING, DOWNSPOUTS, GUTTERS, SOFFIT VENTS AND CONDUCTOR HEADS ARE TO BE FIELD PAINTED U.N.O.
- ALL COLOR AND MATERIAL CHANGES WILL OCCUR AT INSIDE CORNERS UNLESS OTHERWISE NOTED.
- FOR DOOR, WINDOW AND STOREFRONT SCHEDULE, SEE SHEETS A-810 THRU A-840. REFER TO SHEET A-009 FOR STC ACOUSTICAL REQUIREMENTS.
- PROVIDE TEMPERED SAFETY GLAZING AT ALL HAZARDOUS LOCATIONS AS SPECIFIED IN CBC SECTIONS 2406.4.1 THRU 2406.4.7. SEE SCHEDULES ON SHEETS SERIES A-800
- FOR TYPICAL PANEL SIDING WALL ASSEMBLY DETAILS SEE SHEET A-911 & A-912

07.02 FIBER-CEMENT SIDING NO. 2, "HARDIE LAP SIDING" FIELD PAINTED COLOR: KELLY MOORE RIDING BOOTS - KMA64
09.01 CEMENT PLASTER NO. 1, SAND FLOAT 20/30 FINISH, COLOR: KELLY MOORE ADOBE WHITE - HLS4201
09.46 EXTERIOR TYPE X GYP SHEATHING

- WINDOW TAG
- STOREFRONT TAG
- CEMENT PLASTER - WHITE
- CEMENT PLASTER - DARK BROWN
- CEMENT PLASTER - BEIGE
- ENHANCED PLASTER
- LAP SIDING - WHITE
- LAP SIDING - BROWN

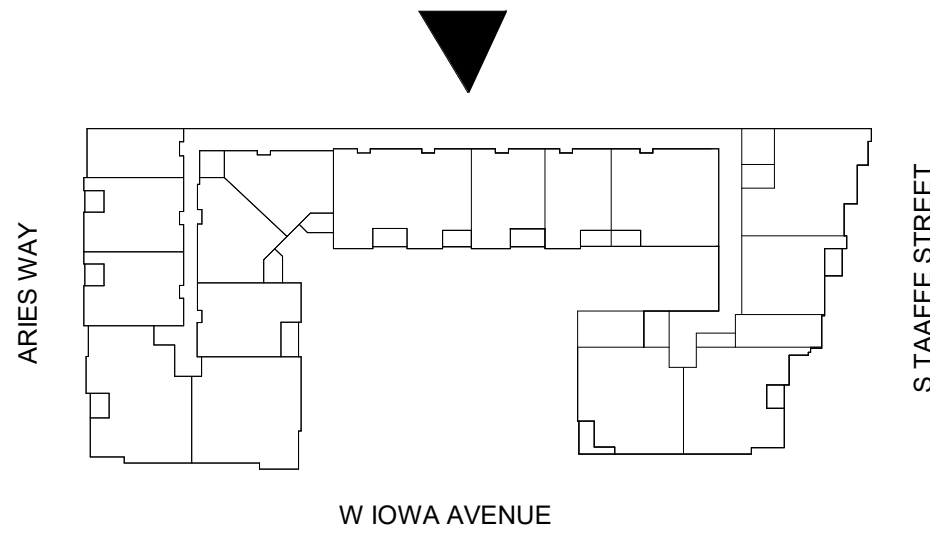

EXTERIOR ELEVATION NOTES

EXTERIOR ELEVATION KEY NOTES

EXTERIOR ELEVATION LEGEND

KEYPLAN