



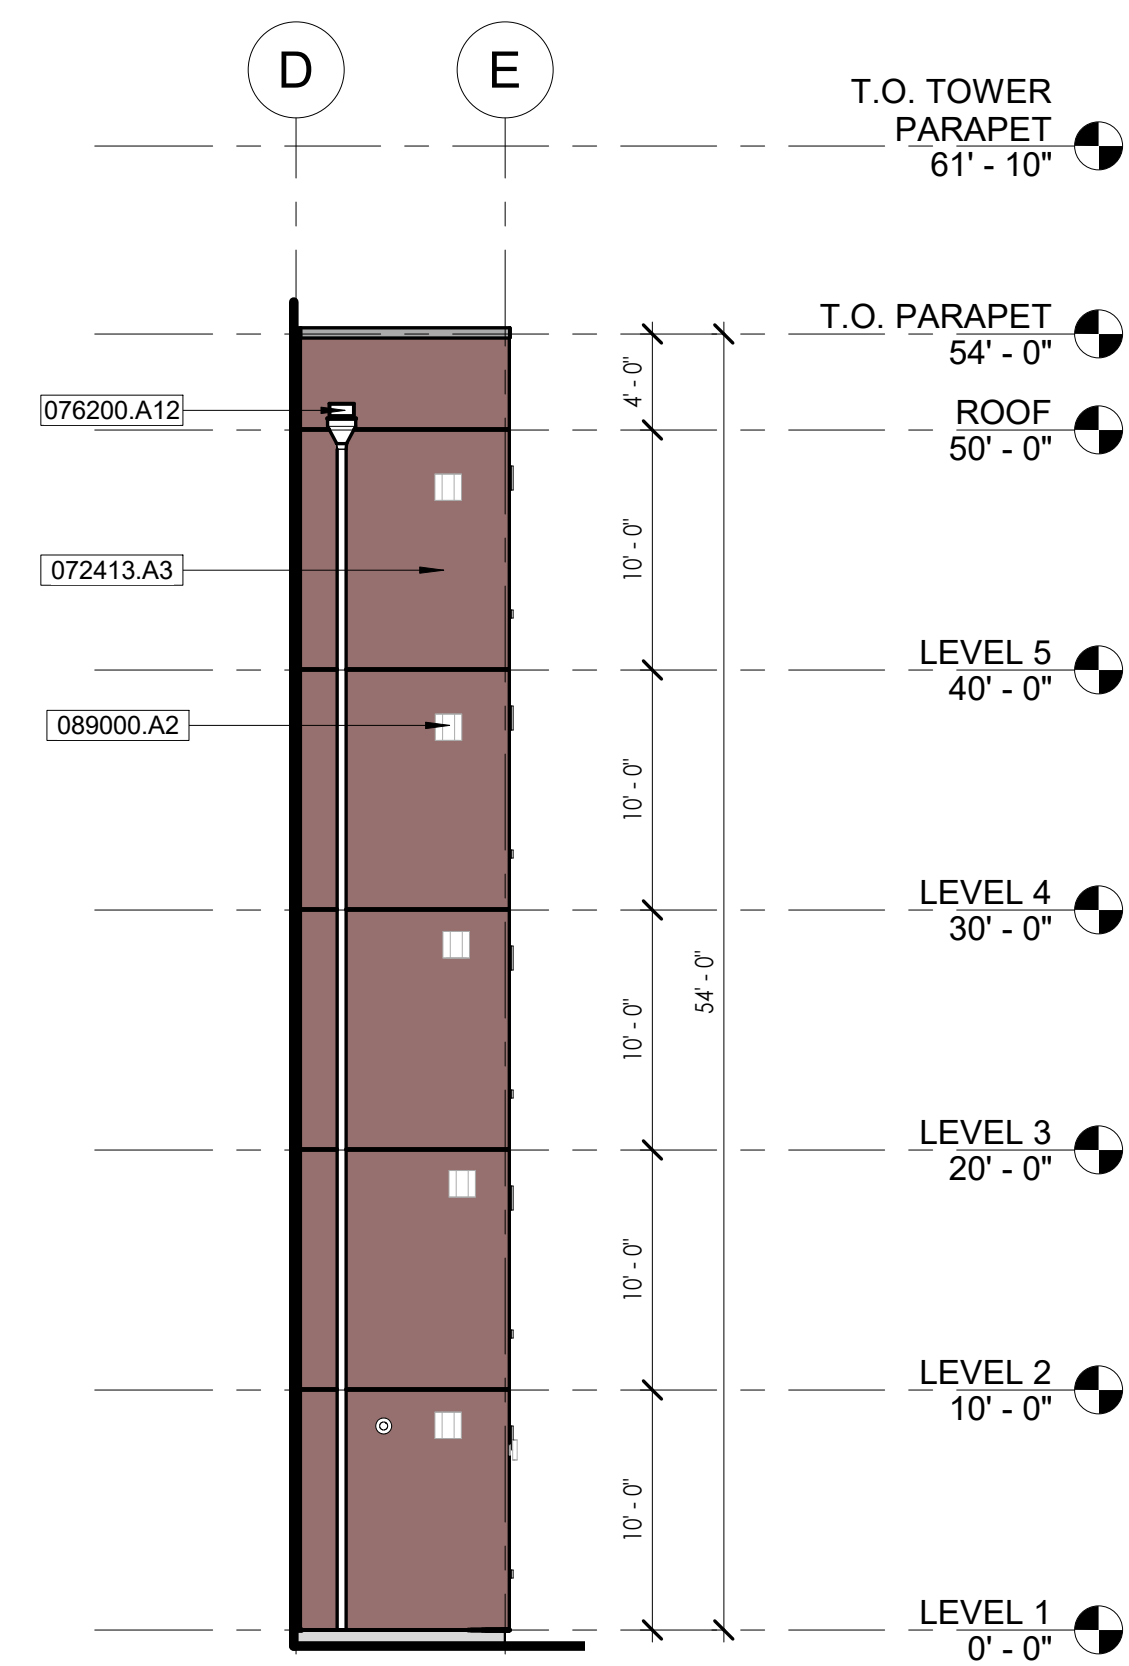

NORTH WING - RETURN ELEVATION - WEST ELEVATION	SCALE 1/8" = 1'-0"	3
---	-----------------------	---

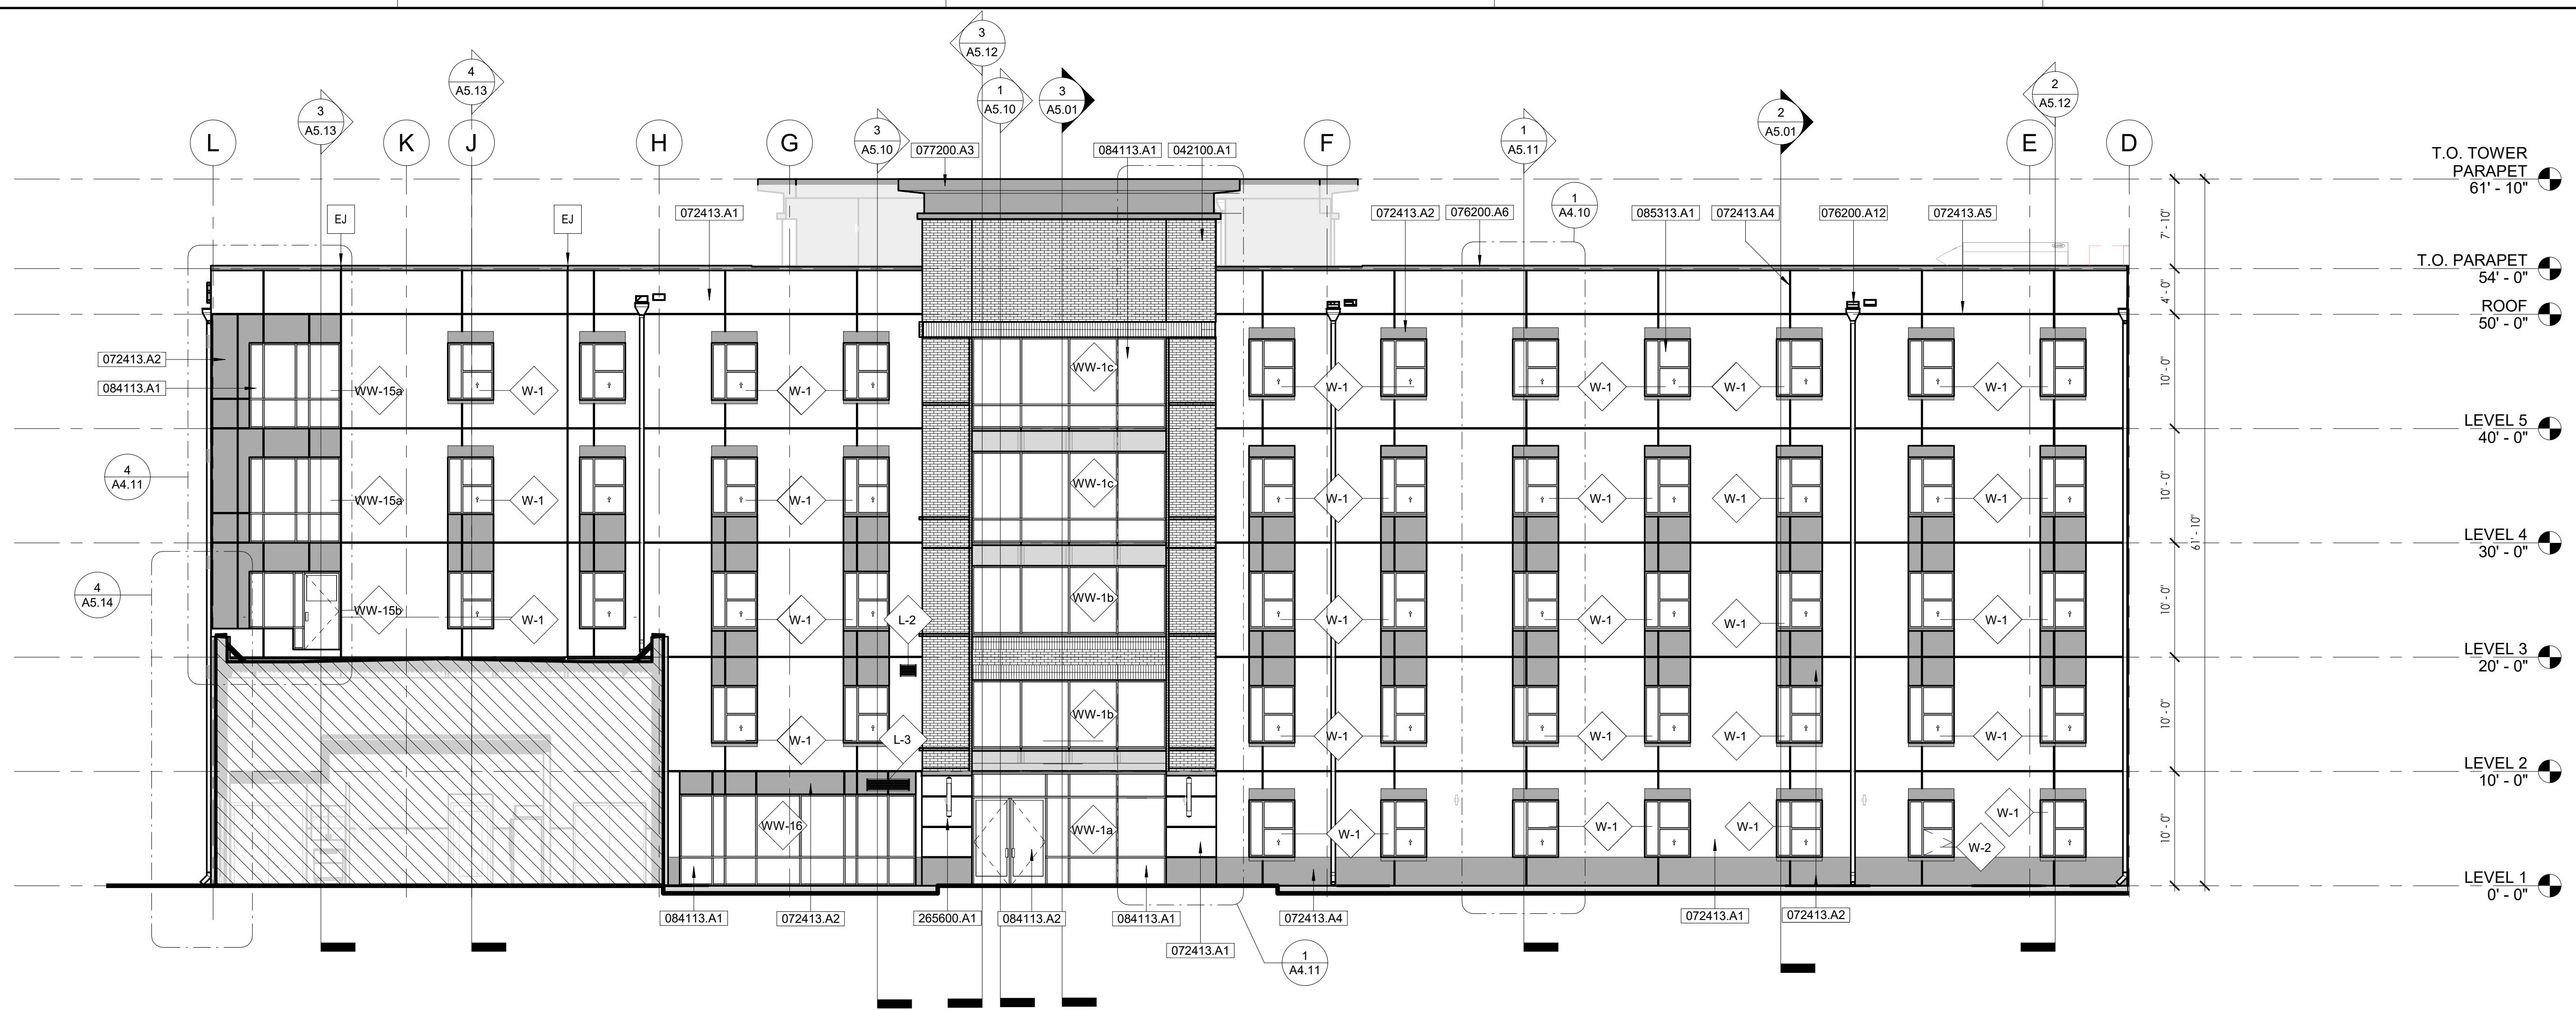

MAIN ENTRY/SOUTH WING - EAST ELEVATION	SCALE 1/8" = 1'-0"	1
--	-----------------------	---



NORTH WING - EAST ELEVATION	SCALE 1/8" = 1'-0"	4
-----------------------------	-----------------------	---




NORTH WING - SOUTH ELEVATION	SCALE 1/8" = 1'-0"	2
------------------------------	-----------------------	---

KEYNOTES


042070.1	Full brick veneer to match existing campus profile. Basis of Design:
042082.2	Solid Surface Countertop W/ integral 4" Splash
072413.1	EIFS. Color: 1.0 White-118 the exterior acrylic-based polymer topcoat. Textured finish w/ reinforcing mesh. Provide impact resistant mesh 60 AFF @ plaza conditions - Basis of Design: Stothorn C. Mineral
072413.2	EIFS. Color: 2. Gray-118 the exterior acrylic-based polymer topcoat. Textured finish w/ reinforcing mesh. Provide impact resistant mesh 60 AFF @ plaza conditions - Basis of Design: Stothorn C. Mineral
072413.3	EIFS. Color: 3. Brick Red-118 the exterior acrylic-based polymer topcoat. Textured finish w/ reinforcing mesh. Provide impact resistant mesh 60 AFF @ plaza conditions - Basis of Design: Stothorn C. Mineral
072413.4	EIFS aesthetic relief, recess in insulation. Ref. A149-42
072413.5	EIFS expansion joint @ top of floor slab and edge on conc. where typ. (h) Ref. 8.9.1 & 8.9.2
072413.1	Metal Panel - Concealed Fastener - Basis of Design: Austin Systems
072413.2	Metal Panel, Vertical Revealed Fin. Ref. Detail 1119-42
072602.1	25 gage galvanized crimped steel over 1/2" x 30" (Grage U) underlayment
072602.6	25 gage galvanized Wall Cap. Polyurethane Coating
072602.12	385 Pre-finished 24 gage galvanized steel through-wall support
072720.3	Prefinished extruded aluminum cornice. 4674 x 457 W.
084113.1	Aluminum Trough Drainage - See Window Schedule - Basis of Design: Arcadco Tc60
084113.2	Aluminum Trough Drainage - See Door and Window Schedule
085331.1	Vinyl Flanged Window, See Window Schedule - Basis of Design: Miquard Tuscaney Series, Book Frame, Series 8220
085331.1	Extruded Aluminum Stationary Low Drainable Base by Greenheck ESD-603
085401.2	Engraved Vent 8" exhaust hood draft. Ref. Mechanical Drawings
255600.1	Surface Mounted Light Fixture See Electrical Drawings

KEY PLAN

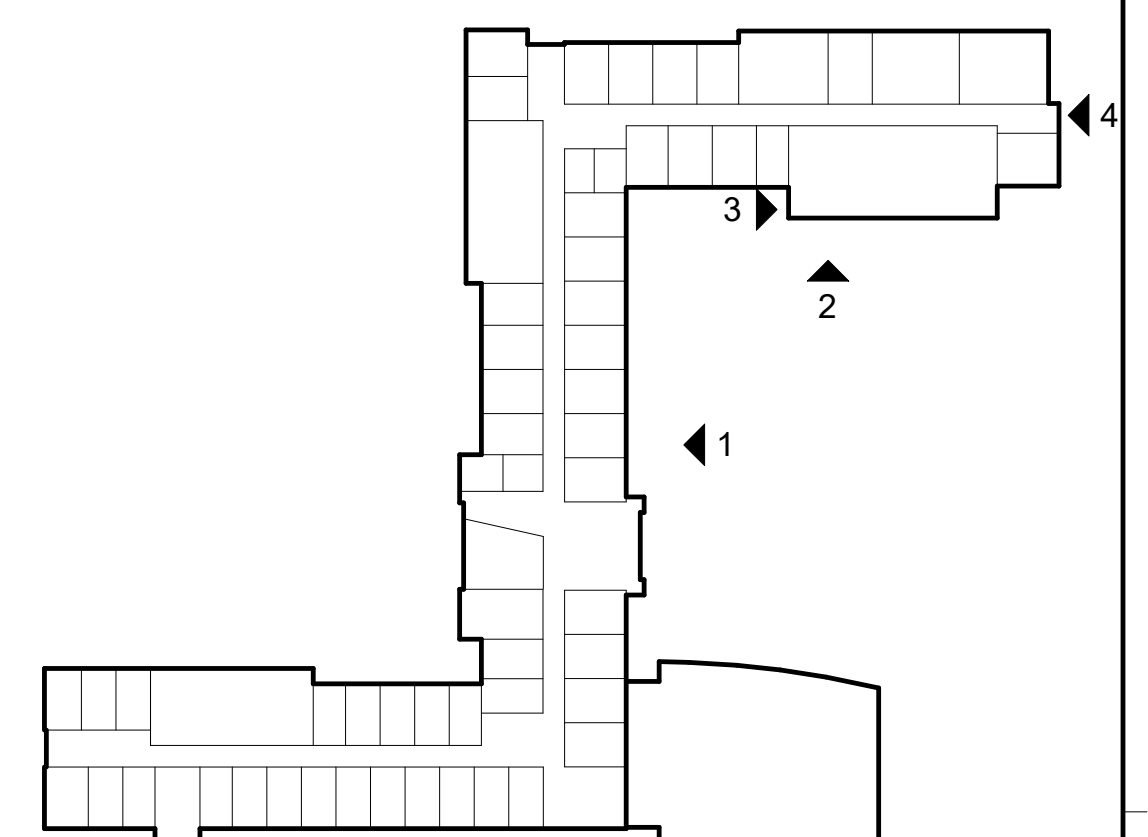

www.hpiarchitecture.com
15 22nd street
Newport Beach, CA 92663
o: 949.675.6442

SEAL

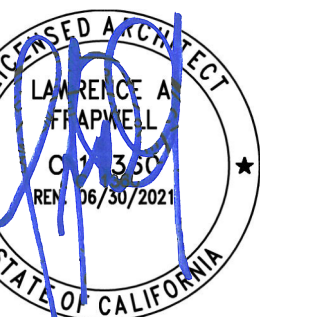

CONSULTANTS

PROJECT TITLE
RJC - STUDENT HOUSING
INCREMENT 2

501 Mendocino Ave, Santa Rosa, CA 95401

[illegible]

PROJECT IDENTIFICATION

THE DRAWINGS IN THE SHEET INDEX WERE ORIGINALLY CREATED IN
AUTODESK REVIT V. 2018 UNLESS OTHERWISE NOTED.

THE ORIGINAL SIZE OF THIS SHEET IS 30" X 42".

THESE DRAWINGS AND SPECIFICATIONS ARE THE PROPERTY AND COPYRIGHT OF THE ARCHITECT AND SHALL NOT BE USED ON ANY OTHER PROJECT OR LOCATIONS EXCEPT AS DESCRIBED ON THE DRAWINGS, WITHOUT WRITTEN AGREEMENT WITH THE ARCHITECT.

© HPI ARCHITECTURE 2020

SHEET TITLE


EXTERIOR ELEVATIONS

SHEET NUMBER


A4.01

CONSTRUCTION DOCUMENTS
NOT FOR CONSTRUCTION


2020-03-12 5:04:20 PM BM 360/358-CC-RC-Student Housing_820.rvt

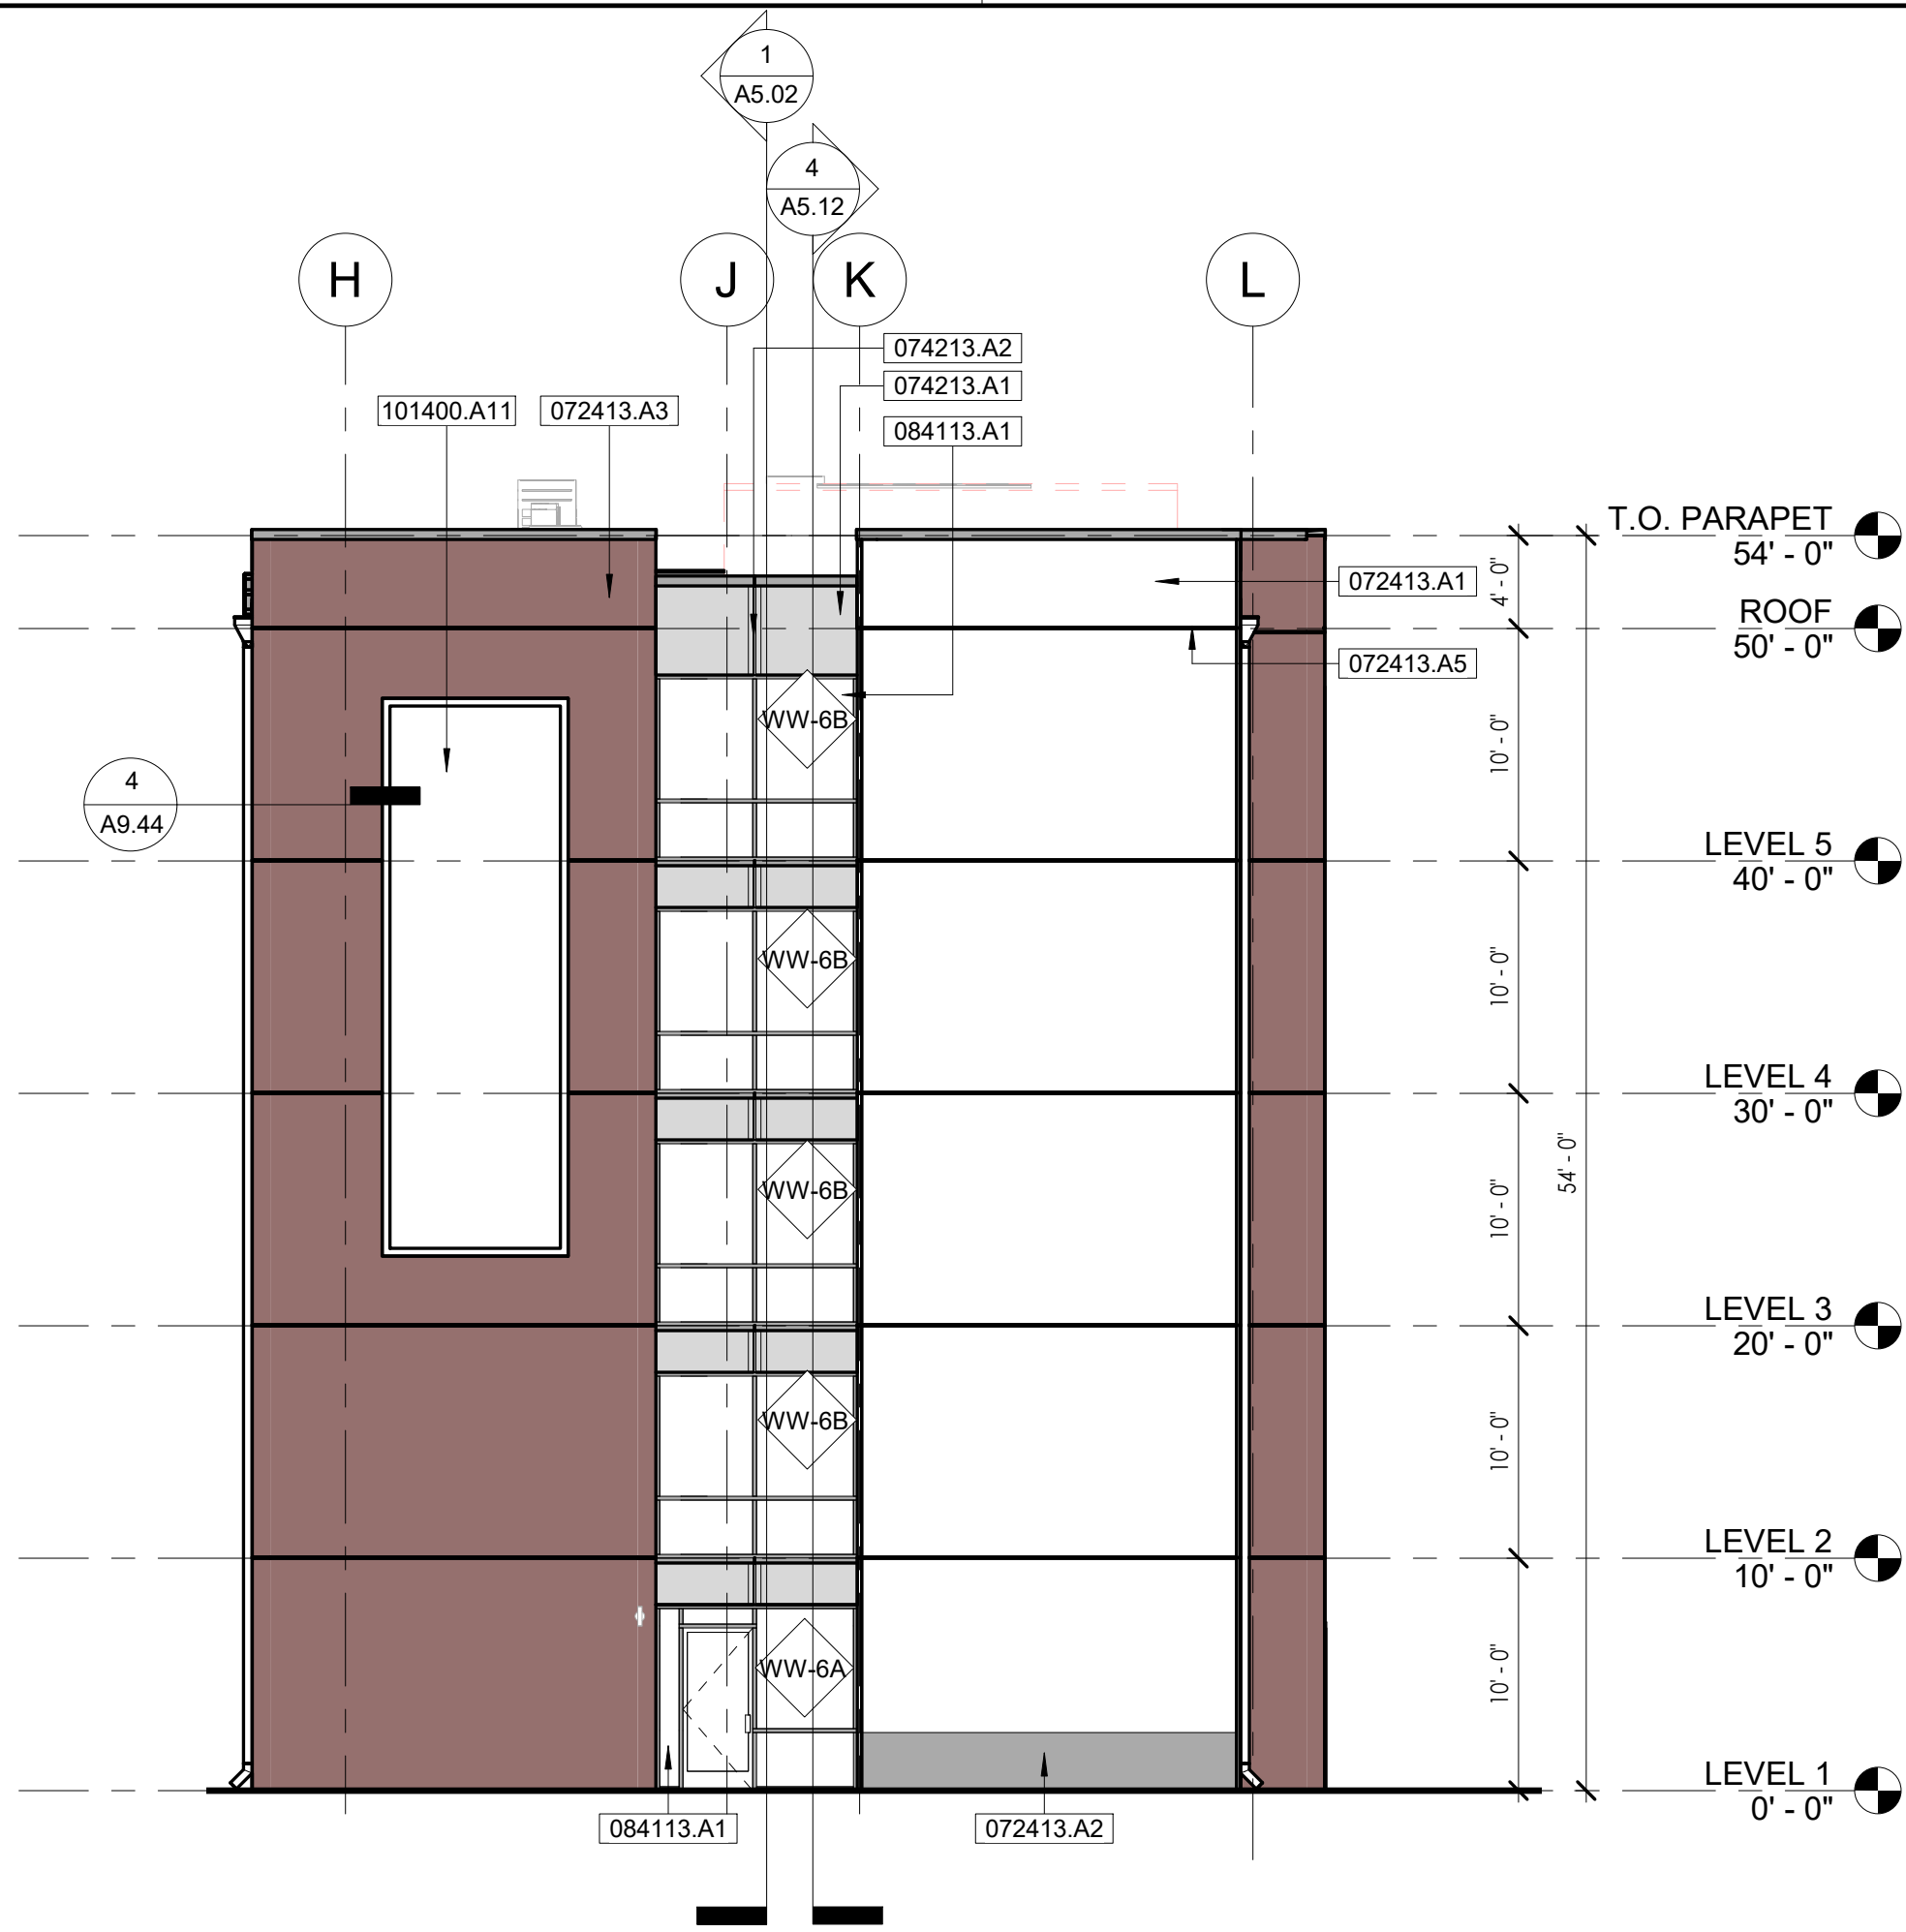

SOUTH WING - WEST ELEVATION SCALE 1/8" = 1'-0" 2

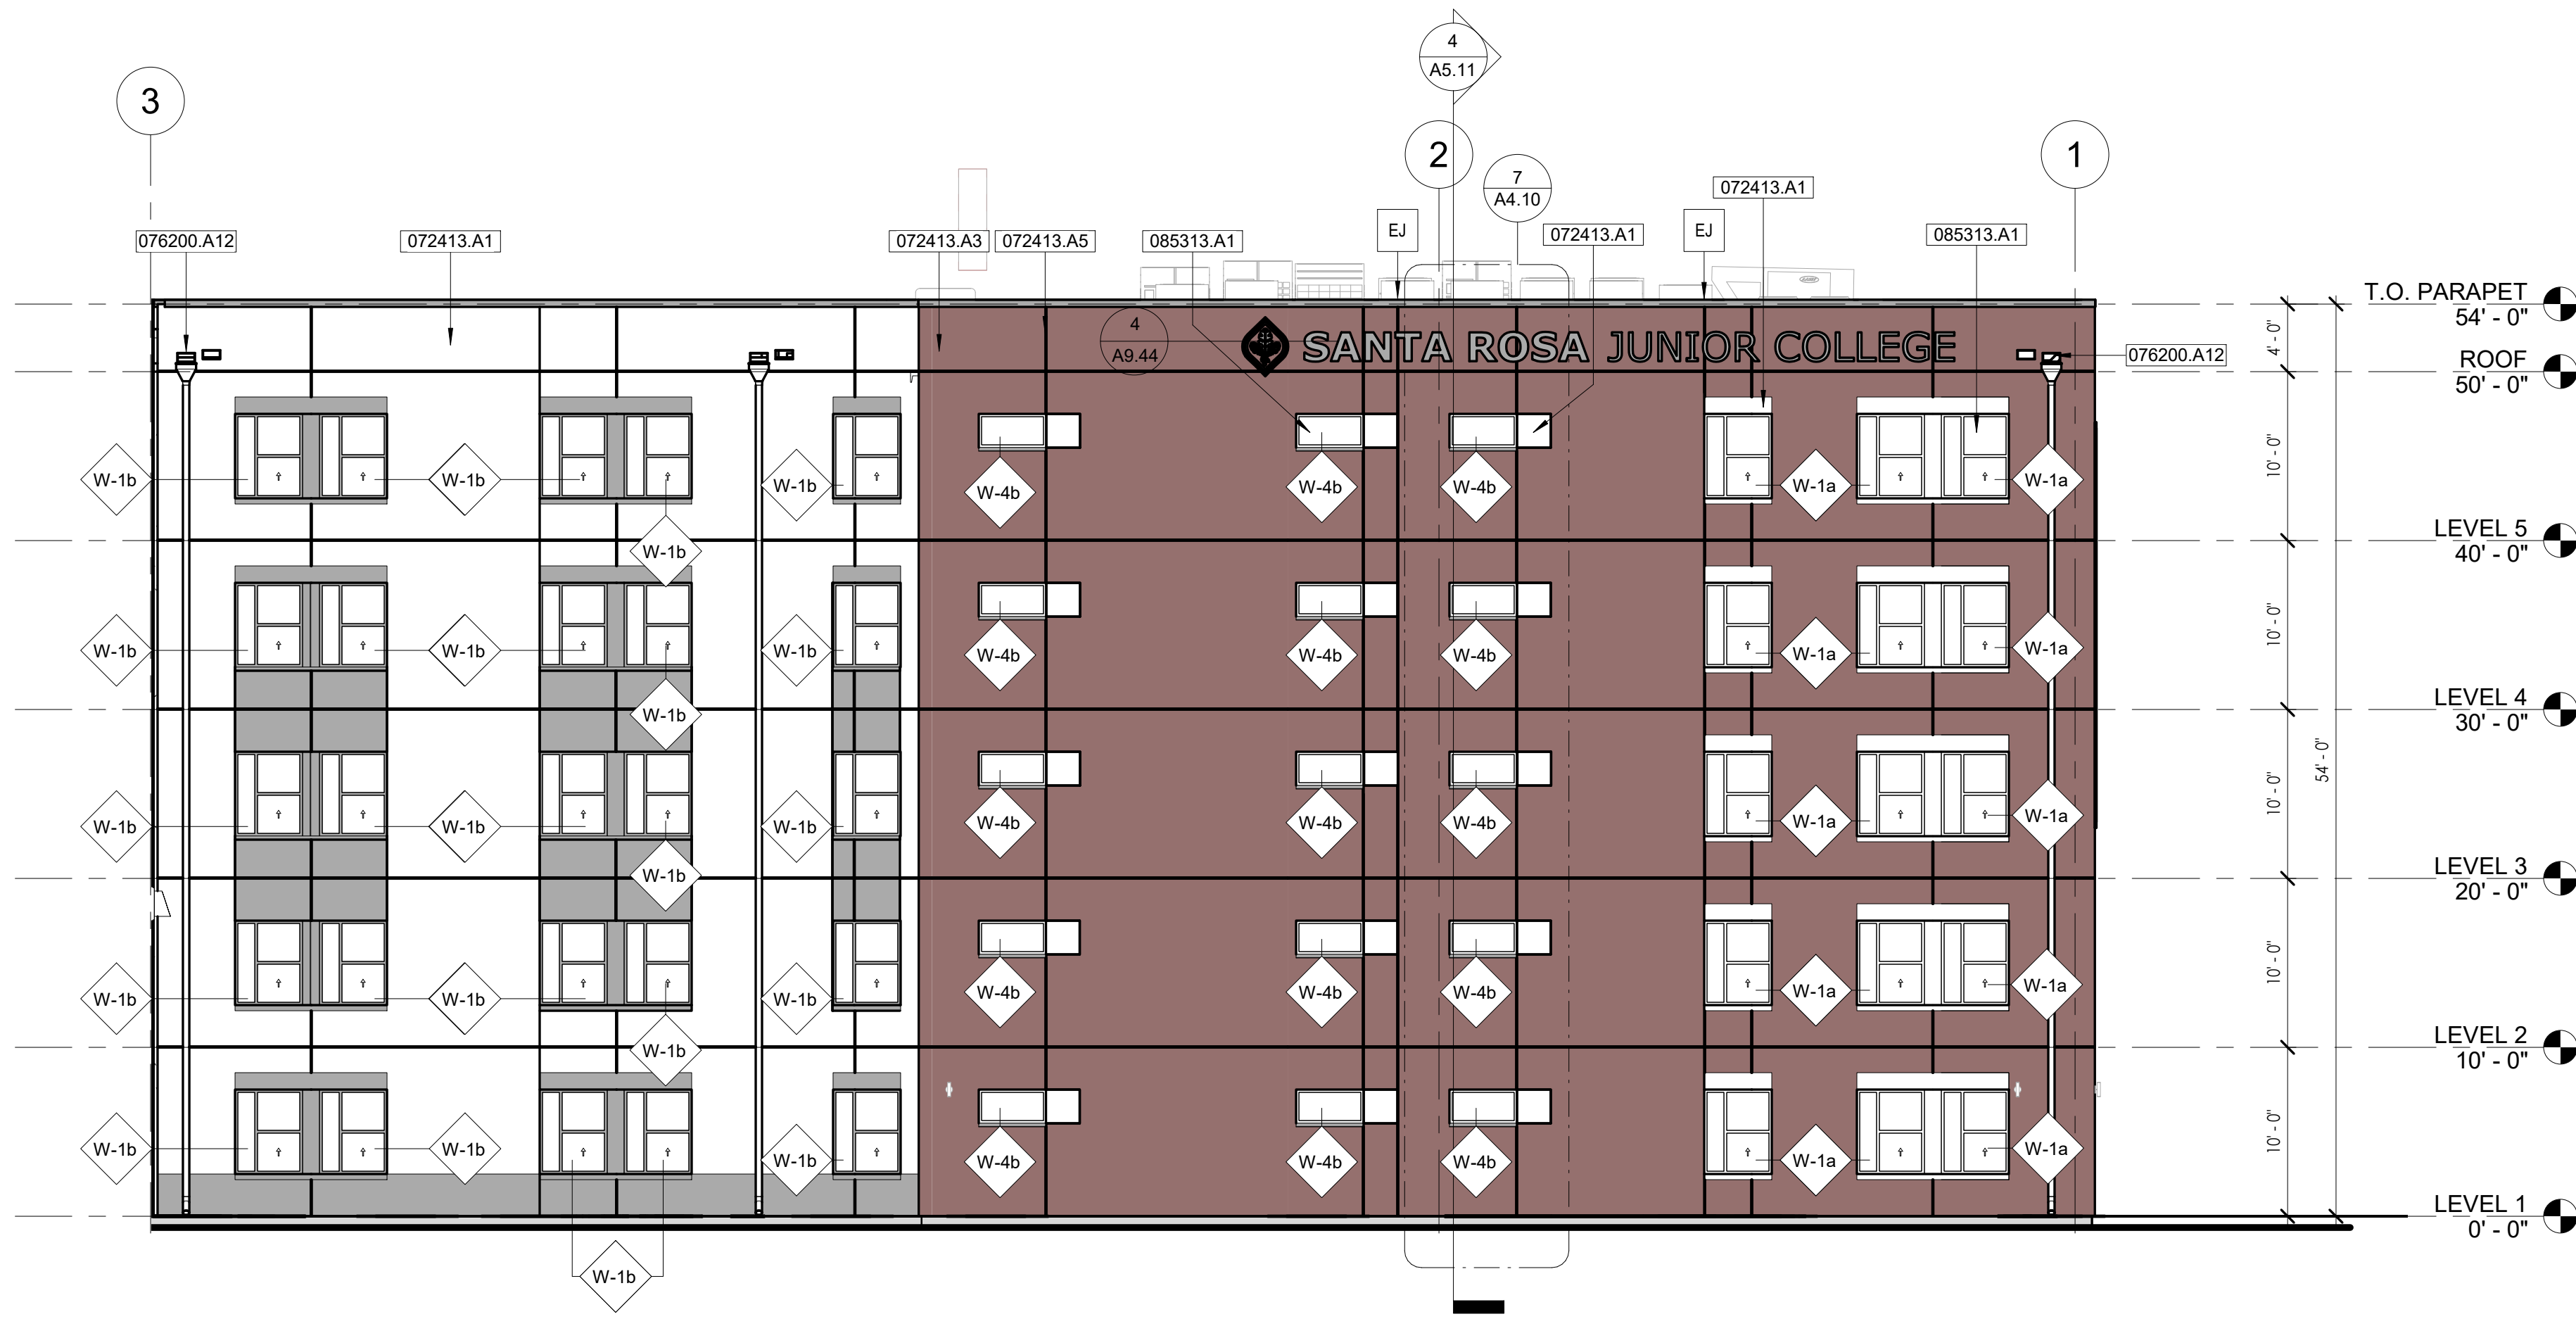

SOUTH WING - NORTH ELEVATION SCALE 1/8" = 1'-0" 1

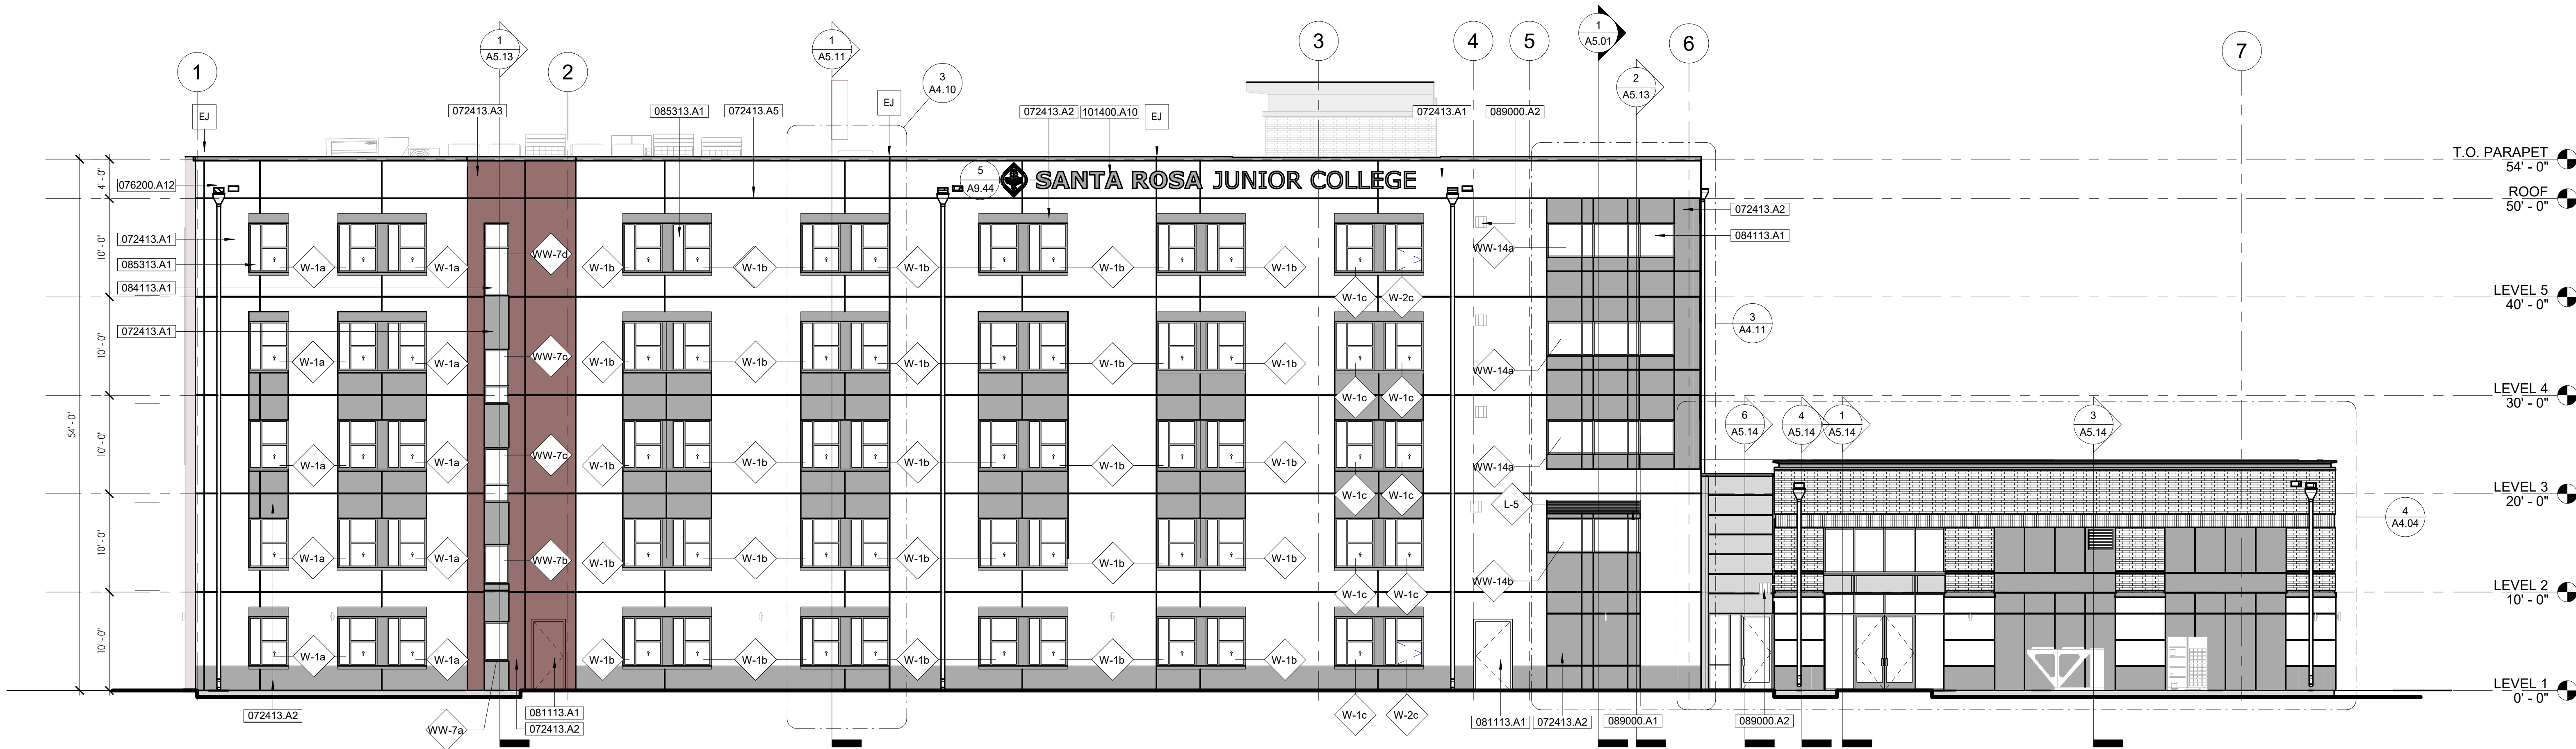


SOUTH WING - SOUTH ELEVATION SCALE 1/8" = 1'-0" 3

KEYNOTES

072413.A1	EPS, Color 1: Off-White, 1/8" thick exterior acrylic-based polymer topcoat, textured finish w/ reinforcing mesh. Provide impact resistant mesh 60" AFF @ plaza conditions - Basis of Design: Stothen CI Mineral
072413.A2	EPS, Color 2: Gray, 1/8" thick exterior acrylic-based polymer topcoat, textured finish w/ reinforcing mesh. Provide impact resistant mesh 60" AFF @ plaza conditions - Basis of Design: Stothen CI Mineral
072413.A3	EPS, Color 3: Brick Red, 1/8" thick exterior acrylic-based polymer topcoat, textured finish w/ reinforcing mesh. Provide impact resistant mesh 60" AFF @ plaza conditions - Basis of Design: Stothen CI Mineral
072413.A5	EPS expansion joint @ top of floor slab and edges on conc. shear walls (typ.) Ref. 8.9 & 10/A9.42
072413.A1	Metal Panel - Concealed Fastener - Basis of Design: Martin F-Series
072413.A2	Metal Panel, Vertical Reveal Trim, Ref. Detail 11/A9.42
072620.A12	SBS Pre-Bonded 24 gauge galvanized steel through-wall scupper
081113.A1	Painted hollow metal door and frame per schedule
084113.A1	Aluminum Storefront/Window Wall System, See Window Schedule - Basis of Design: Arcadia TC670
085313.A1	Vinyl Flanged Window, See Window Schedule - Basis of Design: Milguard Tuscan Series, Black Frame, Series 8220
089000.A1	Extruded Aluminum Stationary Louver Drainable Blade by Greenheck ESD-603
089000.A2	Exhaust Venti @ exhaust hood duct, Ref. Mechanical drawings
101400.A10	Cast Aluminum College Logo- Verify design and location w/ Architect, Ref. 3/A9.44
101400.A11	Building Signage Frame 8x24'- Verify banner design with university, Basis of Design: BannerGrip, Ref. 2/A9.44

KEY PLAN

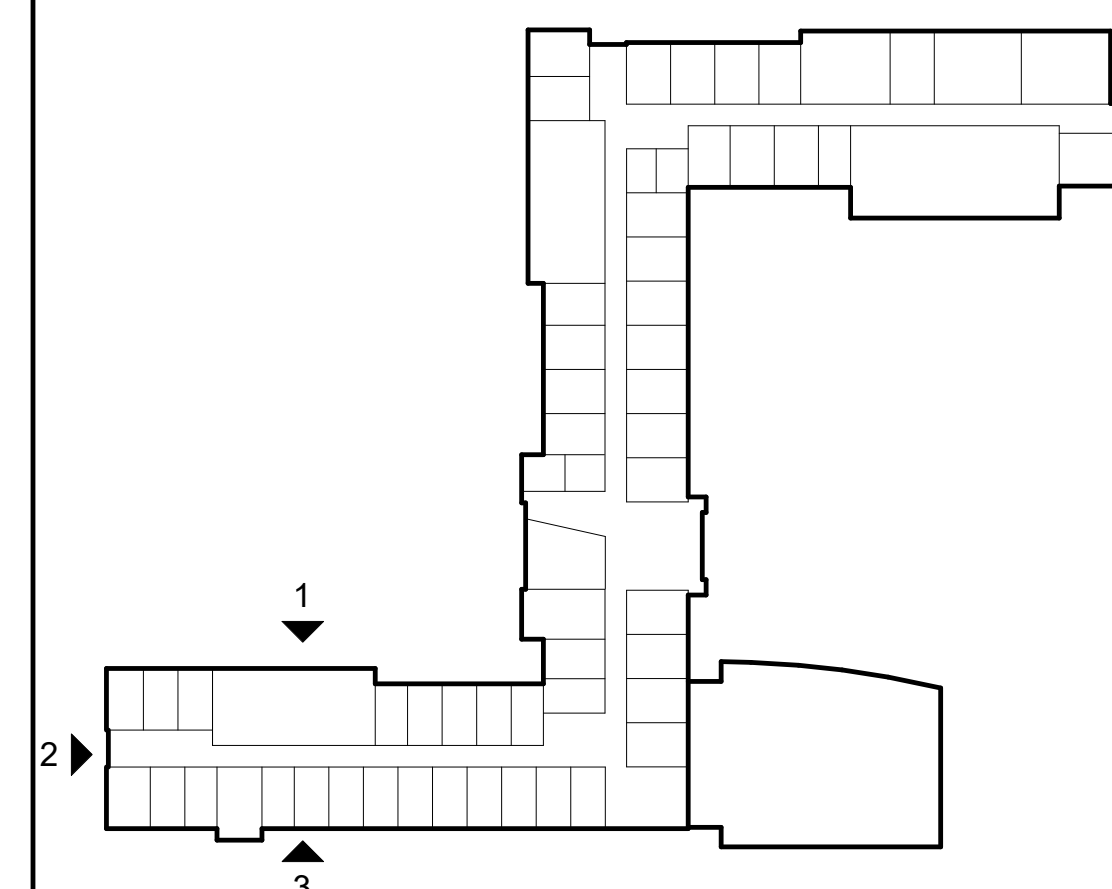

DSA STAMP



www.hpiarchitecture.com
115 22nd street
Newport Beach, CA 92663
o: 949.675.6442

SEAL



CONSULTANTS

PROJECT TITLE
SRJC - STUDENT HOUSING
INCREMENT 2

1501 Mendocino Ave, Santa Rosa, CA 95401



SERVITAS
COLLEGIATE REAL ESTATE SERVICES

ISSUED		
#	DATE	DESCRIPTION
1	2020-03-12	DSA SUBMITTAL
2		
3		
4		
5		
6		
7		
8		
9		
10		
11		
12		
13		
14		
15		
16		
17		
18		
19		
20		

PROJECT IDENTIFICATION
THE DRAWINGS IN THE SHEET INDEX WERE ORIGINALLY CREATED IN AUTOCAD REVIT V. 2018 UNLESS OTHERWISE NOTED.
THE ORIGINAL SIZE OF THIS SHEET IS 36" X 42".

THESE DRAWINGS AND SPECIFICATIONS ARE THE PROPERTY AND COPYRIGHT OF THE ARCHITECT AND SHALL NOT BE USED ON ANY OTHER PROJECT OR LOCATIONS EXCEPT AS DESCRIBED ON THE DRAWINGS WITHOUT WRITTEN AGREEMENT WITH THE ARCHITECT.

© HPI ARCHITECTURE 2020

SHEET TITLE

EXTERIOR ELEVATIONS

SHEET NUMBER

A4.03

CONSTRUCTION DOCUMENTS
NOT FOR CONSTRUCTION

Technical drawing of a cross-section of a building facade, showing the parapet and roof structure. The drawing includes dimensions and labels for various components:

- Dimensions:**
 - Overall height: 11' - 10"
 - Parapet height: 7' - 10"
 - Roof height: 4' - 0"
 - Roof slope: 50° - 0"
- Labels and Callouts:**
 - 075423 A1**: Label for the parapet structure.
 - 076200 A11**: Label for the parapet structure.
 - 081113 A1**: Label for the parapet structure.
 - 077200 A3**: Label for the parapet structure.
 - 3 A5.01**: Callout for the parapet structure.
 - 1 A5.10**: Callout for the parapet structure.
 - 3 A5.10**: Callout for the parapet structure.
- Structural Elements:**
 - T.O. TOWER PARAPET 61' - 10"**: Top of Tower Parapet.
 - T.O. PARAPET 54' - 0"**: Top of Parapet.
 - ROOF 50° - 0"**: Roof structure.

[illegible]

042010.01	Full brick veneer to match existing course palette. Basis of Design:
042010.03	Double brick soldier course
072413.01	EIFS, Color: 1-Off White, 1/8" thick exterior acrylic-based polymer topcoat, textured finish w/ reinforcing mesh. Provide impact resistant mesh #6 ATF in plaza conditions - Basis of Design: Statham C Mineral
072413.02	EIFS, Color: 2-Gray, 1/8" thick exterior acrylic-based polymer topcoat, textured finish w/ reinforcing mesh. Provide impact resistant mesh #6 ATF in plaza conditions - Basis of Design: Statham C Mineral
072413.03	Metal Panel - Concealed Fastener - Basis of Design: Morin F-Series
072413.04	Metal Panel, Vertical Recessed Joint, Detail 11A/5.42
075423.01	100 Membrane Roofing over 1/4" Cover Board
076020.02	22 gauge galvanized coping, polyurethane coating, ø/30 mil [Graze Ultra] underlayment
076200.01	3" x 4" pre-manufactured Aluminum downspout-color to be selected by Architect
076200.02	58" dia. finished 24 gauge galvanized steel through-wall scupper
077200.03	Prefinished extruded aluminum cornice, 47 1/2" x 8" W.
077200.04	Prefinished extruded aluminum cornice, 11 1/2" x 8" W.
079500.02	Seismic Joint Wall by Construction Specialists [Basis of Design]
081113.01	Painted hollow metal door and frame per schedule
083313.01	Horizontal bi-folding door - Basis of Design: Accada Bifold 10000 Series
084113.01	Aluminum Storefront Window Wall System, See Window Schedule - Basis of Design: Accada T400
084113.02	Aluminum Storefront Door, See Door and Window Schedule
089000.01	Extruded Aluminum Stationary Low Drainable Baffle by Greenheck ESD-603

SCALE
1/4" = 1'-0"

Architectural section drawing of a building facade. The drawing shows five levels (LEVEL 1 to LEVEL 5), a ROOF, and a T.O. PARAPET. The drawing includes dimensions for heights and widths, and labels for various components like windows and doors.

Dimensions (Left Side):

- Overall height: 54'-0"
- Level 1 height: 10'-0"
- Level 2 height: 10'-0"
- Level 3 height: 10'-0"
- Level 4 height: 10'-0"
- Level 5 height: 10'-0"
- Roof height: 4'-0"
- Parapet height: 4'-0"

Dimensions (Right Side):

- Level 1 height: 10'-0"
- Level 2 height: 20'-0"
- Level 3 height: 20'-0"
- Level 4 height: 30'-0"
- Level 5 height: 40'-0"
- Roof height: 50'-0"
- Parapet height: 54'-0"

Labels and Components:

- 7 (Top Left)
- 2 A5.11 (Top Center)
- 072413.A1 (Window Label)
- 076200.A6 (Window Label)
- EJ (Door Label)
- T.O. PARAPET 54'-0"
- ROOF 50'-0"
- 072413.A1 (Window Label)
- 085313.A1 (Window Label)
- 072413.A3 (Window Label)
- LEVEL 5 40'-0"
- LEVEL 4 30'-0"
- LEVEL 3 20'-0"
- LEVEL 2 10'-0"
- LEVEL 1 0'-0"

SCALE
1/4" = 1'-0"

[illegible]

SCALE
1/4" = 1'-0"

Architectural section drawing of a building facade, showing levels 1 through 5, a roof, and a parapet. The drawing includes dimensions and material callouts.

Dimensions (from top to bottom):

- 4'-0"
- 4'-0"
- 2'-2"
- 5'-0"
- 2'-10"
- 10'-0"
- 10'-0"
- 10'-0"
- 10'-0"
- 10'-0"
- 10'-0"
- 2'-6"
- 5'-0"
- 2'-6"

Levels and Features:

- T.O. PARAPET 54' - 0"**
- ROOF 50' - 0"**
- LEVEL 5 40' - 0"**
- LEVEL 4 30' - 0"**
- LEVEL 3 20' - 0"**
- LEVEL 2 10' - 0"**
- LEVEL 1 0' - 0"**

Material Callouts:

- 076200.A6
- 072413.A2
- 085313.A1
- 072413.A1
- 072413.A4
- 072413.A5
- 072413.A2
- 072413.A2

Other Annotations:

- 1'-0" (twice)
- 4"
- 1'-6"
- 1'-5"

SCALE
1/4" = 1'-0"

072413.A1	EFS, Color 1: Off-White, 1/8" the exterior acrylic-based polymer topcoat; textured finish w/ reinforcing mesh. Provide impact resistant mesh #6 AFF @ plaza conditions - Basis of Design: Stolhamn CI Mineral
072413.A2	EFS, Color 2: Gray, 1/8" the exterior acrylic-based polymer topcoat; textured finish w/ reinforcing mesh. Provide impact resistant mesh #6 AFF @ plaza conditions - Basis of Design: Stolhamn CI Mineral
072413.A3	EFS, Color 3: Brick Red, 1/8" the exterior acrylic-based polymer topcoat; textured finish w/ reinforcing mesh. Provide impact resistant mesh #6 AFF @ plaza conditions - Basis of Design: Stolhamn CI Mineral
072413.A4	EFS aesthetic reveal, recess in insulation, Ref. A1/A9/A2
072413.A5	EFS exterior joint @ top of floor slab and edges on conc. shear walls (typ.) Ref. 9.8 & 10.49/A2
076200.A4	22 gauge unpainted galv. Coat. Polyurethane Coating
085313.A1	Vinyl Flanged Window, See Window Schedule - Basis of Design: Milgroud Lutyens Series, Block Frame, Series 8220



architecture
Design
Collective

www.hpiarchitecture.com
 115 22nd street
 Newport Beach, CA 92663
 o: 949.675.6442

1501 Mendocino Ave, Santa Rosa, CA 95401



SERVITAS
COLLEGIATE REAL ESTATE SERVICES

[illegible]

PROJECT IDENTIFICATION

THE DRAWINGS IN THE SHEET INDEX WERE ORIGINALLY CREATED IN AUTOCAD REVIT V. 2018 UNLESS OTHERWISE NOTED.

THE ORIGINAL SIZE OF THIS SHEET IS 30" X 42".

THESE DRAWINGS AND SPECIFICATIONS ARE THE PROPERTY AND COPYRIGHT OF THE ARCHITECT AND SHALL NOT BE USED ON ANY OTHER PROJECT OR LOCATIONS EXCEPT AS DESCRIBED ON THE DRAWINGS, WITHOUT WRITTEN AGREEMENT WITH THE ARCHITECT.

© HPI ARCHITECTURE 2020

SHEET TITLE

ENLARGED EXTERIOR
ELEVATIONS

SHEET NUMBER

A4.10

CONSTRUCTION DOCUMENTS
NOT FOR CONSTRUCTION

This architectural section drawing illustrates the vertical profile of a building facade, detailing various levels and structural elements. The drawing includes the following components:

- Levels and Heights:**
 - T.O. TOWER PARAPET:** 61' - 10"
 - T.O. PARAPET:** 54' - 0"
 - ROOF:** 50' - 0"
 - LEVEL 5:** 40' - 0"
 - LEVEL 4:** 30' - 0"
 - LEVEL 3:** 20' - 0"
 - LEVEL 2:** 10' - 0"
 - LEVEL 1:** 0' - 0"
- Structural Elements and Annotations:**
 - A5.11:** Located at the top left corner.
 - G:** A circular marker near the top center.
 - 077200.A3:** An annotation pointing to a horizontal structural element near the top.
 - 042100.A3:** An annotation pointing to a horizontal structural element between the Roof and Level 5.
 - 042100.A4:** An annotation pointing to a horizontal structural element on Level 5.
 - 042100.A1:** An annotation pointing to a horizontal structural element on Level 5.
 - 084113.A1:** Two annotations pointing to horizontal structural elements on Level 4.
 - 042100.A3:** An annotation pointing to a horizontal structural element on Level 3.
 - 076200.A2:** An annotation pointing to a horizontal structural element on Level 2.
 - 072413.A2:** Two annotations pointing to horizontal structural elements on Level 1.
 - A4.25:** A circular marker at the bottom left corner.
- Dimensions and Spacing:**
 - Vertical dimensions are indicated by arrows along the right side, corresponding to the level heights.
 - Horizontal dimensions are indicated by arrows along the left side, showing the width of different sections.

Architectural section drawing of a building facade, showing levels 1 through 5, parapets, and various material callouts. The drawing includes vertical dimensions and material specifications.

Levels and Dimensions:

- LEVEL 1:** 0'-0" (Total height from base to Level 1 top)
- LEVEL 2:** 10'-0" (Total height from base to Level 2 top)
- LEVEL 3:** 20'-0" (Total height from base to Level 3 top)
- LEVEL 4:** 30'-0" (Total height from base to Level 4 top)
- LEVEL 5:** 40'-0" (Total height from base to Level 5 top)
- ROOF:** 50'-0" (Total height from base to Roof top)
- T.O. PARAPET:** 54'-0" (Total height from base to Top of Parapet)
- T.O. TOWER PARAPET:** 61'-10" (Total height from base to Top of Tower Parapet)

Material Callouts:

- 077200.A3:** Material callout for the top parapet section.
- 042100.A3:** Material callout for the brickwork on Levels 3, 4, and 5.
- 042100.A1:** Material callout for the brickwork on Levels 2 and 3.
- 084113.A1:** Material callout for the brickwork on Levels 1 and 2.
- 076200.A2:** Material callout for the brickwork on Level 1.
- 072413.A2:** Material callout for the brickwork on Level 1.

Other Dimensions:

- 8'-0":** Vertical dimension for the section between Level 1 and Level 2.
- 10'-0":** Vertical dimension for the section between Level 2 and Level 3.
- 8'-2":** Vertical dimension for the section between Level 3 and Level 4.
- 6'-1'-10":** Vertical dimension for the section between Level 4 and Level 5.
- 8'-0":** Vertical dimension for the section between Level 5 and the Roof.
- 3'-6":** Vertical dimension for the section between the Roof and the T.O. Parapet.
- 7'-10":** Vertical dimension for the section between the T.O. Parapet and the T.O. Tower Parapet.

CONSTRUCTION DOCUMENTS
NOT FOR CONSTRUCTION