


A	-	STANDING SEAM COPPER METAL AWNING
B	-	GREEN GRANITE BASE
C	-	EXISTING FRED TURNER BUILDING RESIDENTIAL ENTRY
D	-	VINYL CLAD WINDOWS
E	-	PLASTER WITH SAND FINISH
F	-	DECORATIVE CORNICE
G	-	METAL RAILING
H	-	COMPOSITE PANELS
I	-	COPPER PANELS
K	-	CORNICE BAND
L	-	CONCRETE PLANTER WITH GLASS PANEL RAILING
M	-	METAL PANELS

Designed by:	_____
Drawn by:	GH
Architect of Record:	Vince Chupka
Date Plotted:	_____
Issue for Pricing / Bidding:	00/00/00
Issue for Permit Application:	00/00/00
Issue for Construction:	00/00/00
Revisions:	_____

#	DATE	COMMENTS
	10/16/2018	1 PLAN CHECK COMMENTS
	12/05/2018	2 PLAN CHECK COMMENTS
	01/14/2019	3 PLAN CHECK COMMENTS

© 2019 by Humphreys & Partners
Architects, L.P.
All Rights Reserved

The architectural works depicted herein are the sole property of Humphreys & Partners Architects, L.P., and may not be constructed or used without the express written permission of Humphreys & Partners Architects, L.P. Permission is granted to modify or reproduce any of the architectural works, including without limitation the construction of any building, is expressed or should be implied from delivery of preliminary drawings or unsealed construction drawings. Permission to construct the building depicted in sealed construction drawings is expressly conditioned on the full and timely payment of all fees otherwise due Humphreys & Partners Architects, L.P., and, in the absence of a written agreement to the contrary, is limited to a one-time use on the site indicated on these plans.

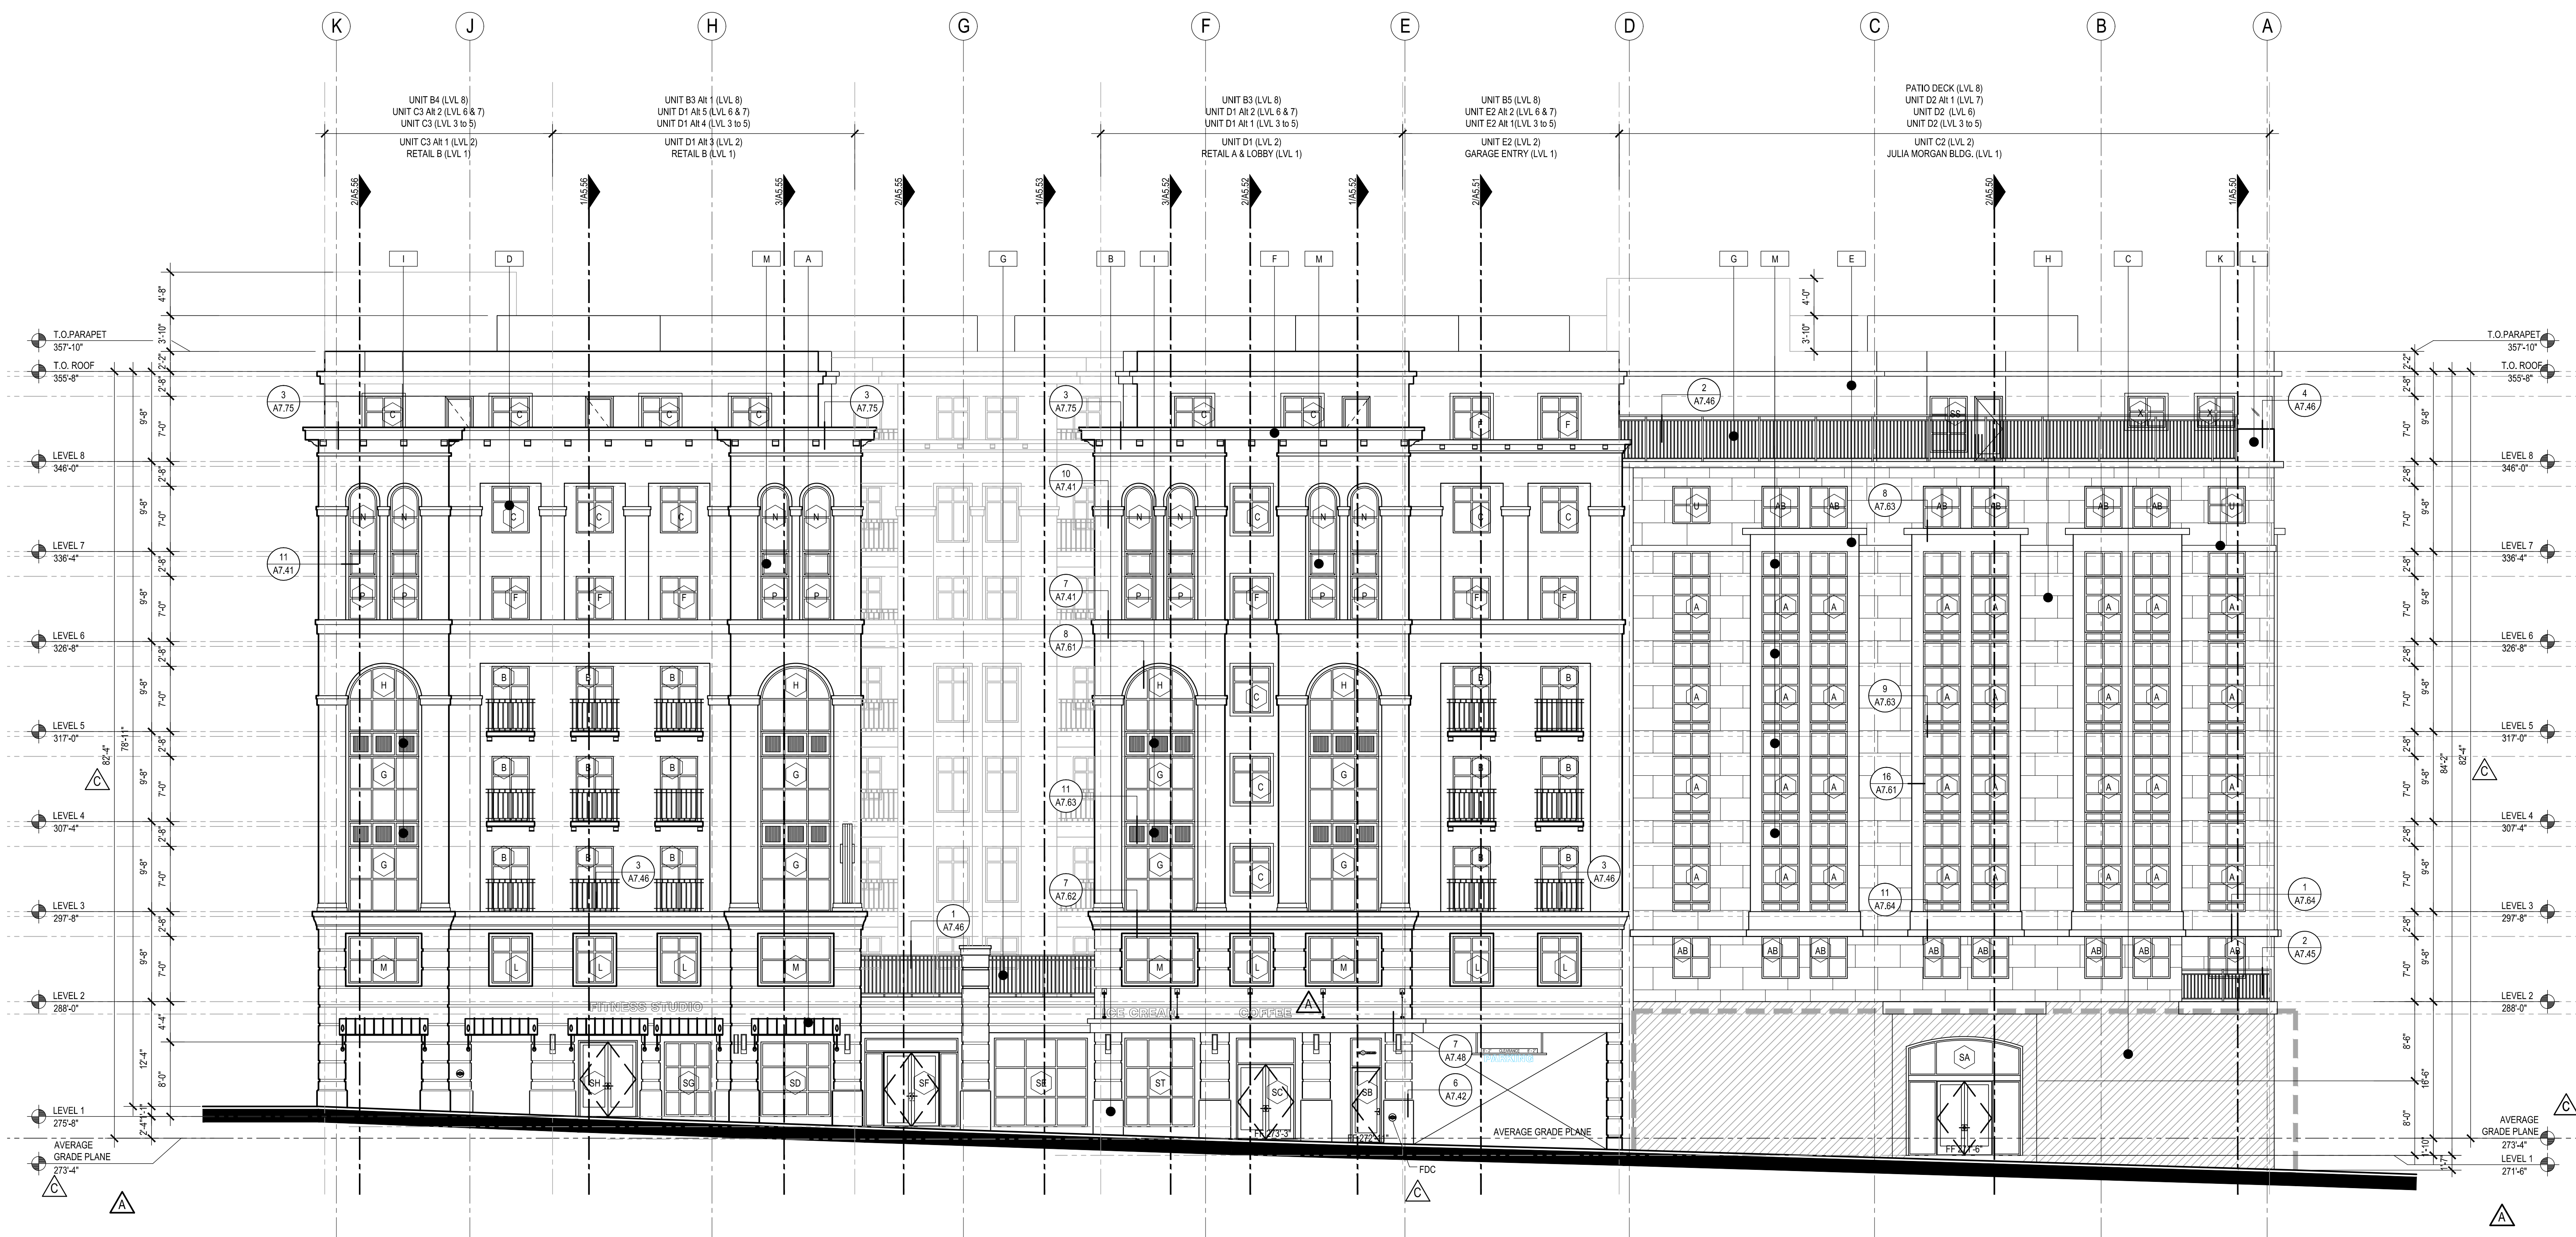

HUMPHREYS & PARTNERS
ARCHITECTS, L.P.

5339 ALPHA ROAD • SUITE 300 • DALLAS, TEXAS 75240
(972) 701-9639 • (972) 701-9639 FAX

DALLAS • CHICAGO • NEW ORLEANS • NEW YORK • NEWPORT BEACH • ORLANDO
SAN RAMON • SCOTSDALE • EDMONTON • TORONTO • MONTEVIDEO
www.humphreys.com



SHEET CONTENTS.

NORTH ELEV.

SHEET NO.


A5.01

15434


FIRST CITY SUBMITTAL 02-01-19

FILE: M:\15434_Landmark-Standard\04_CD\500 ELEV. SECTIONS\A5.01-A5.05-ELEVATIONS.dwg
USER: ghldlgo DATE/TIME: Feb 01, 2019 - 1:50pm
SCALE: 96 LAYOUT: A5.01

FILE: M15434_1 LandmarkStandard04_CD0500_ELEV_SECTIONS\A5.01-A5.05-ELEVATIONS.dwg
USER: ghillegz DATE/TIME: Feb 01, 2019 - 1:50pm
SCALE: 1/8" = 1'-0"

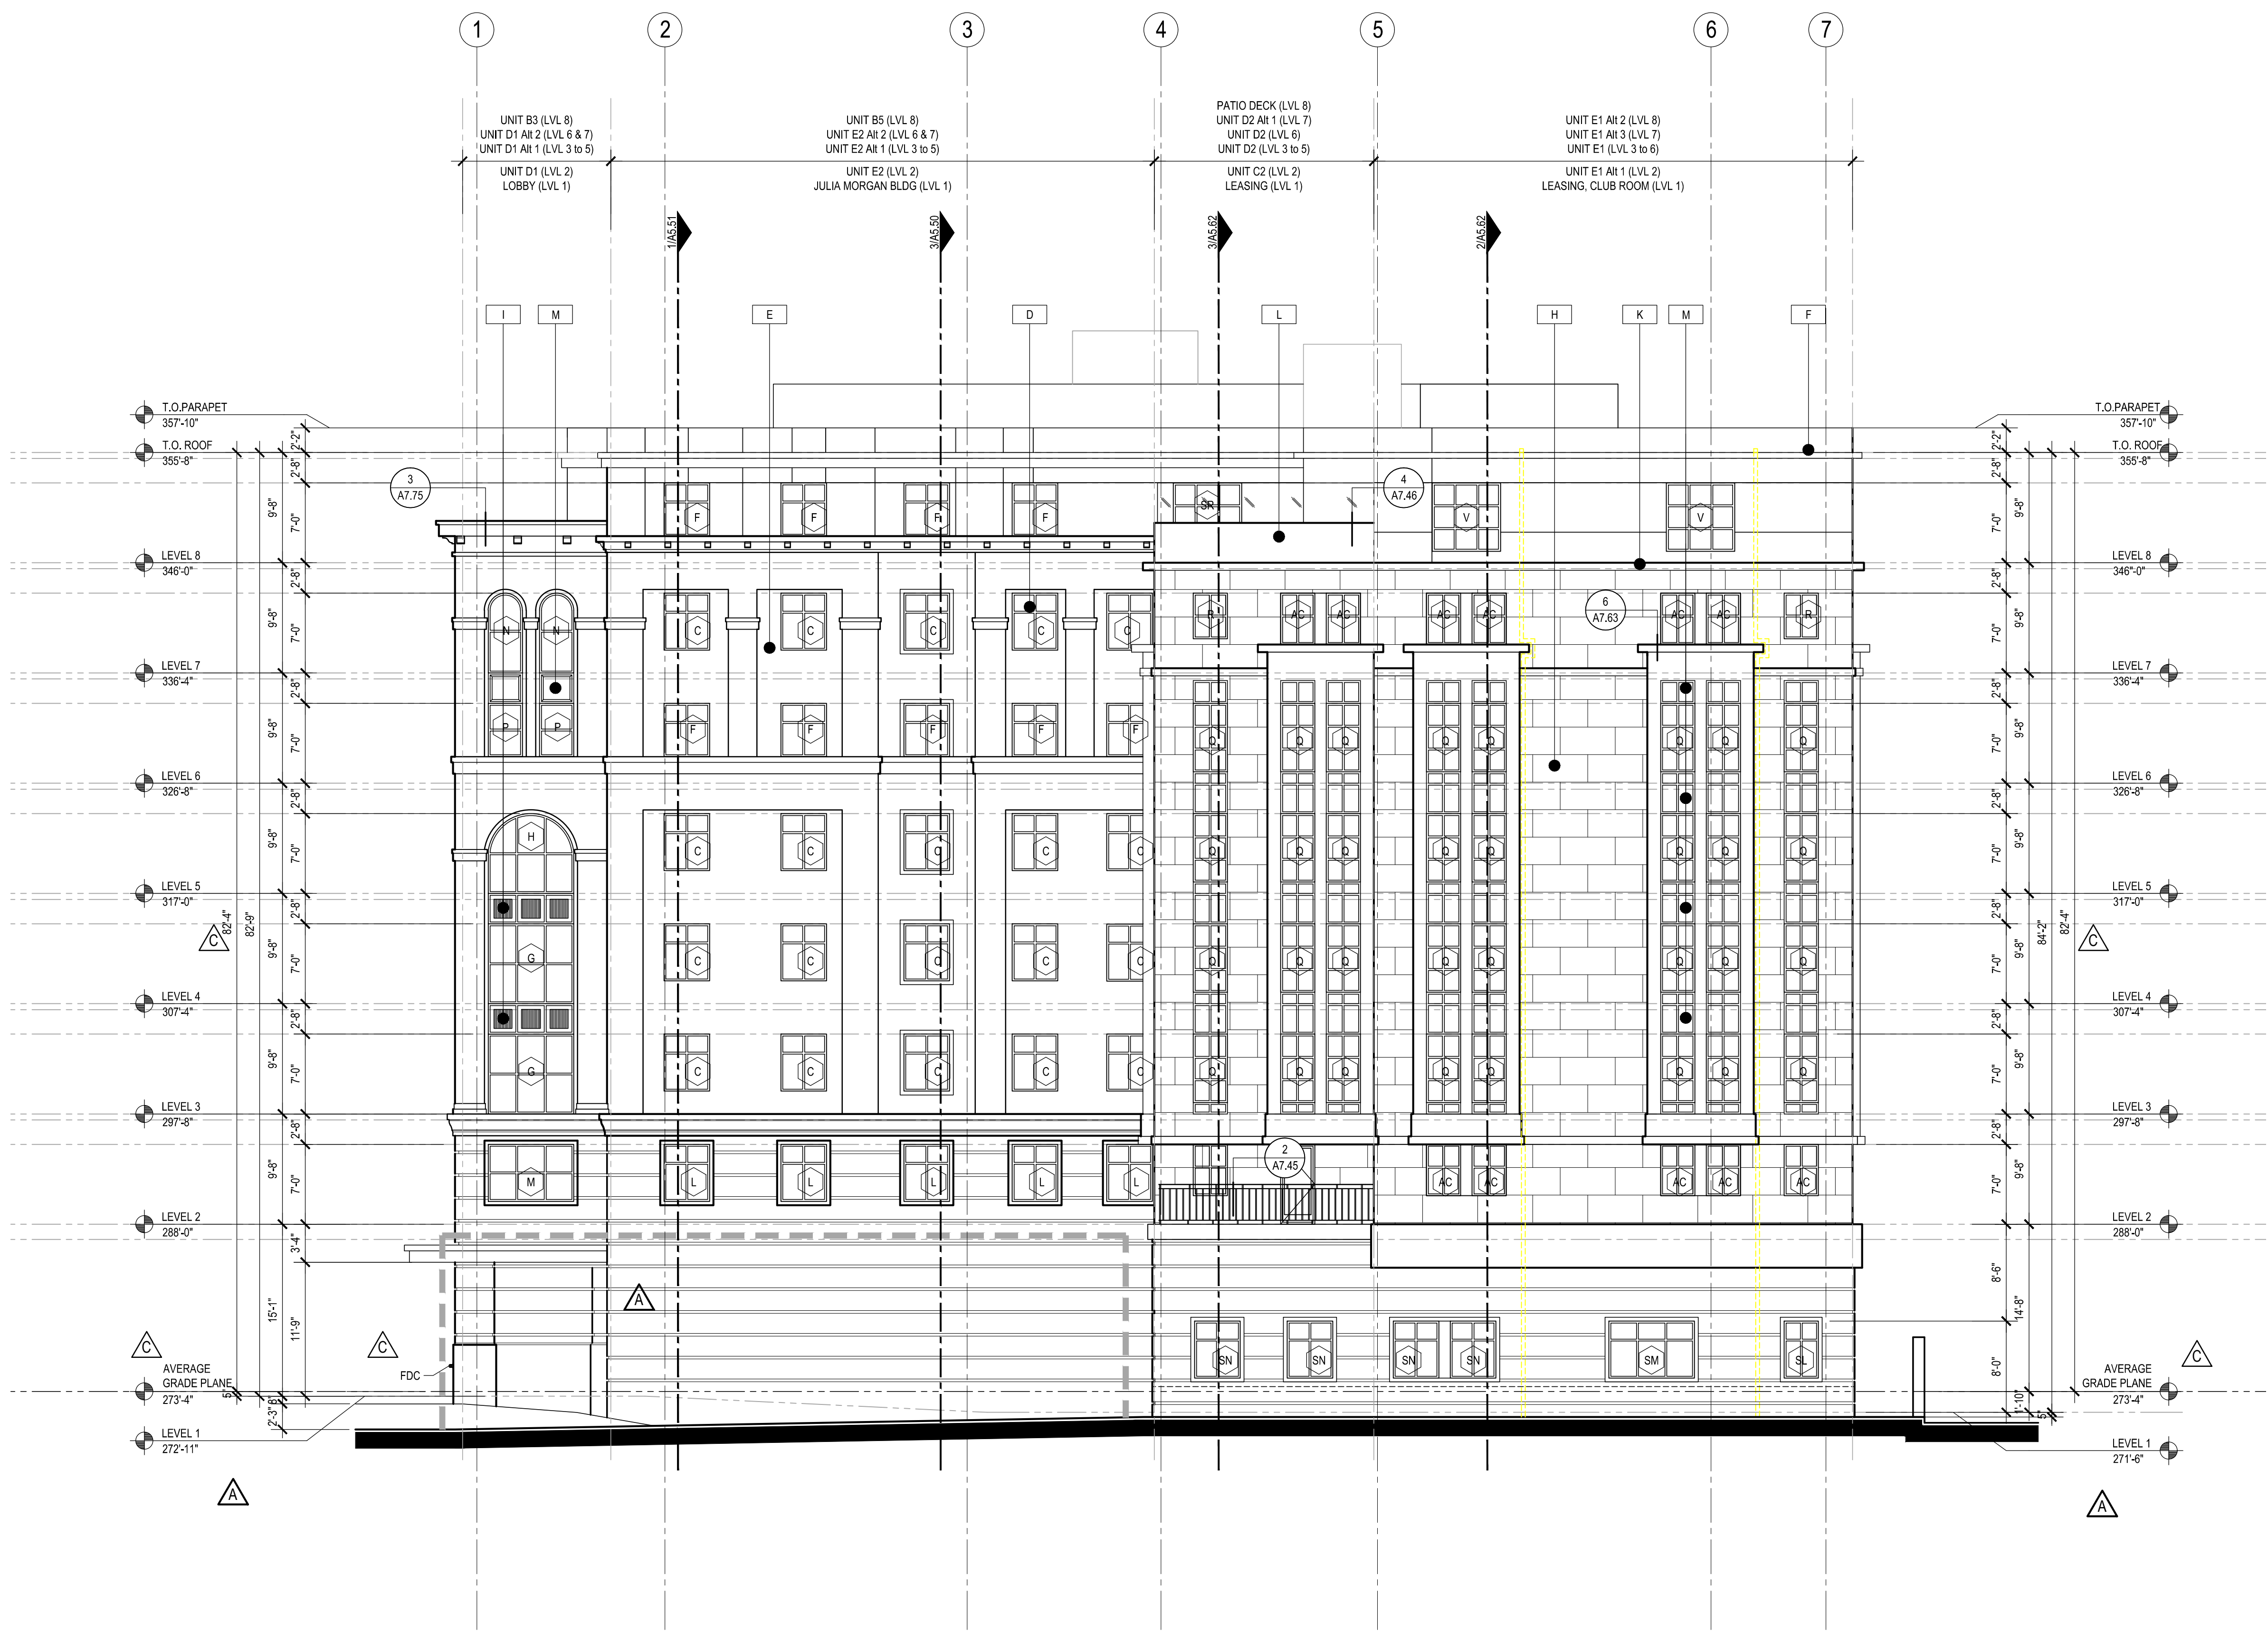

1 WEST ELEVATION
SCALE: 1/8" = 1'-0"

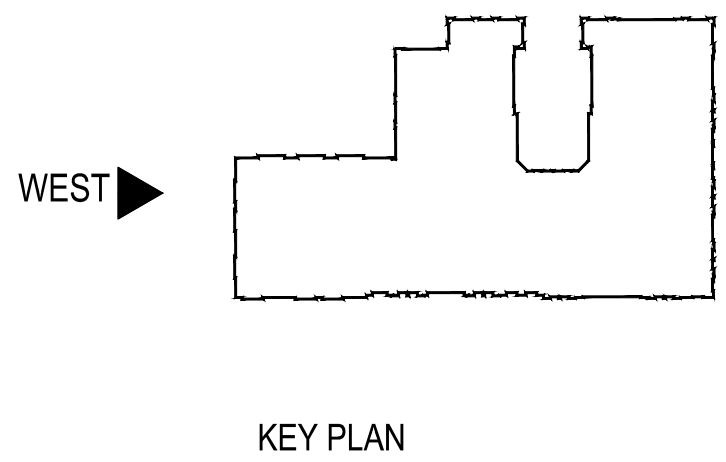

MATERIAL AND COLOR KEYNOTES

- A - STANDING SEAM COPPER METAL AWNING
- B - GREEN GRANITE BASE
- C - EXISTING FRED TURNER BUILDING RESIDENTIAL ENTRY
- D - VINYL CLAD WINDOWS
- E - PLASTER WITH SAND FINISH
- F - DECORATIVE CORNICE
- G - METAL RAILING
- H - COMPOSITE PANELS
- I - COPPER PANELS
- J - CORNICE BAND
- K - CONCRETE PLANTER WITH GLASS PANEL RAILING
- L - METAL PANELS

Designed by:	GH	
Drawn by:	Vince Chupka	
Architect of Record:	Vince Chupka	
Date Plotted:		
Issue for Pricing / Bidding:	00/00/00	
Issue for Permit Application:	00/00/00	
Issue for Construction:	00/00/00	
Revisions:		
#	DATE	COMMENTS
	10/16/2018	1 PLAN CHECK COM
	12/05/2018	2 PLAN CHECK COM
	01/14/2019	3 PLAN CHECK COM

© 2019 by Humphreys & Partners Architects, L.P.
All Rights Reserved
The architectural works depicted herein are the sole property of Humphreys & Partners Architects, L.P. and may not be constructed or used without its express written permission. No permission to modify or reproduce any of the architectural works, including without limitation the construction of any building, is expressed or should be implied from delivery of preliminary drawings or unsealed construction drawings. Permission to construct the building depicted in sealed construction drawings is expressly conditioned on the full and timely payment of all fees otherwise due Humphreys & Partners Architects, L.P. and, in the absence of any written agreement to the contrary, is limited to a one-time use on the site indicated on these plans.

THE STANDARD
BERKELEY, CA
LANDMARK CONSTRUCTION, LLC

HUMPHREYS & PARTNERS
ARCHITECTS, L.P.

5339 ALPHA ROAD - SUITE 300 - DALLAS, TEXAS 75240
(972) 701-9639 / (972) 701-9639 FAX
DALLAS · CHICAGO · NEW ORLEANS · NEW YORK · NEWPORT BEACH · ORLANDO
SAN RAMON · SCOTTSDALE · EDMONTON · TORONTO · MONTEVIDEO
www.humphreys.com



SHEET CONTENTS:
WEST ELEVATION
SHEET NO.

A5.02

15434

FIRST CITY SUBMITTAL 02-01-19

FILE: M15434_Standard04_CD500_ELEV_SECTIONS\A5.01_A5.05-ELEVATIONS.dwg
USER: phillips DATE/TIME: Feb 01, 2019 1:50pm
SCALE: 1/8" = 1'-0"



1 SOUTH ELEVATION
SCALE: 1/8" = 1'-0"

MATERIAL AND COLOR KEYNOTES

- A - STANDING SEAM COPPER METAL AWNING
- B - GREEN GRANITE BASE
- C - EXISTING FRED TURNER BUILDING RESIDENTIAL ENTRY
- D - VINYL CLAD WINDOWS
- E - PLASTER WITH SAND FINISH
- F - DECORATIVE CORNICE
- G - METAL RAILING
- H - COMPOSITE PANELS
- I - COPPER PANELS
- J - CORNICE BAND
- K - CONCRETE PLANTER WITH GLASS PANEL RAILING
- M - METAL PANELS

Designed by:	GH	
Drawn by:	GH	
Architect of Record:	Vince Chupka	
Date Plotted:		
Issue for Pricing / Bidding:	00/00/00	
Issue for Permit Application:	00/00/00	
Issue for Construction:	00/00/00	
Revisions:	00/00/00	
#	DATE	COMMENTS
1	10/16/2018	1 PLAN CHECK COMMENTS.
2	12/05/2018	2 PLAN CHECK COMMENTS.
3	01/14/2019	3 PLAN CHECK COMMENTS.

© 2019 by Humphreys & Partners Architects, L.P.
All Rights Reserved
The architectural works depicted herein are the sole property of Humphreys & Partners Architects, L.P. and may not be constructed or used without its express written permission. No permission to modify or reproduce any of the architectural works, including without limitation the construction of any building, is expressed or should be implied from delivery of preliminary drawings or unsealed construction drawings. Permission to construct the building depicted in sealed construction drawings is expressly conditioned on the full and timely payment of all fees otherwise due Humphreys & Partners Architects, L.P. and, in the absence of any written agreement to the contrary, is limited to a one-time use on the site indicated on these plans.

THE STANDARD
BERKELEY, CA
LANDMARK CONSTRUCTION, LLC

HUMPHREYS & PARTNERS
ARCHITECTS, L.P.
5339 ALPHA ROAD - SUITE 300 - DALLAS, TEXAS 75240
(972) 701-9639 / (972) 701-9639 FAX
DALLAS, CHICAGO, NEW ORLEANS, NEW YORK, NEWPORT BEACH, OCEANO
SAN ANTONIO, SCOTTSDALE, EDMONTON, TORONTO, MONTEVIDEO
www.humphreys.com




SHEET CONTENTS:
SOUTH ELEVATION
SHEET NO.

A5.03

15434

FIRST CITY SUBMITTAL 02-01-19

FILE: M15434_LandmarkStandard04_CD0500_ELEV_SECTIONS\A5.01_A5.05-ELEVATIONS.dwg
USER: ghilguy DATE/TIME: Feb 01, 2019 1:50pm
SCALE: 1/8" = 1'-0"

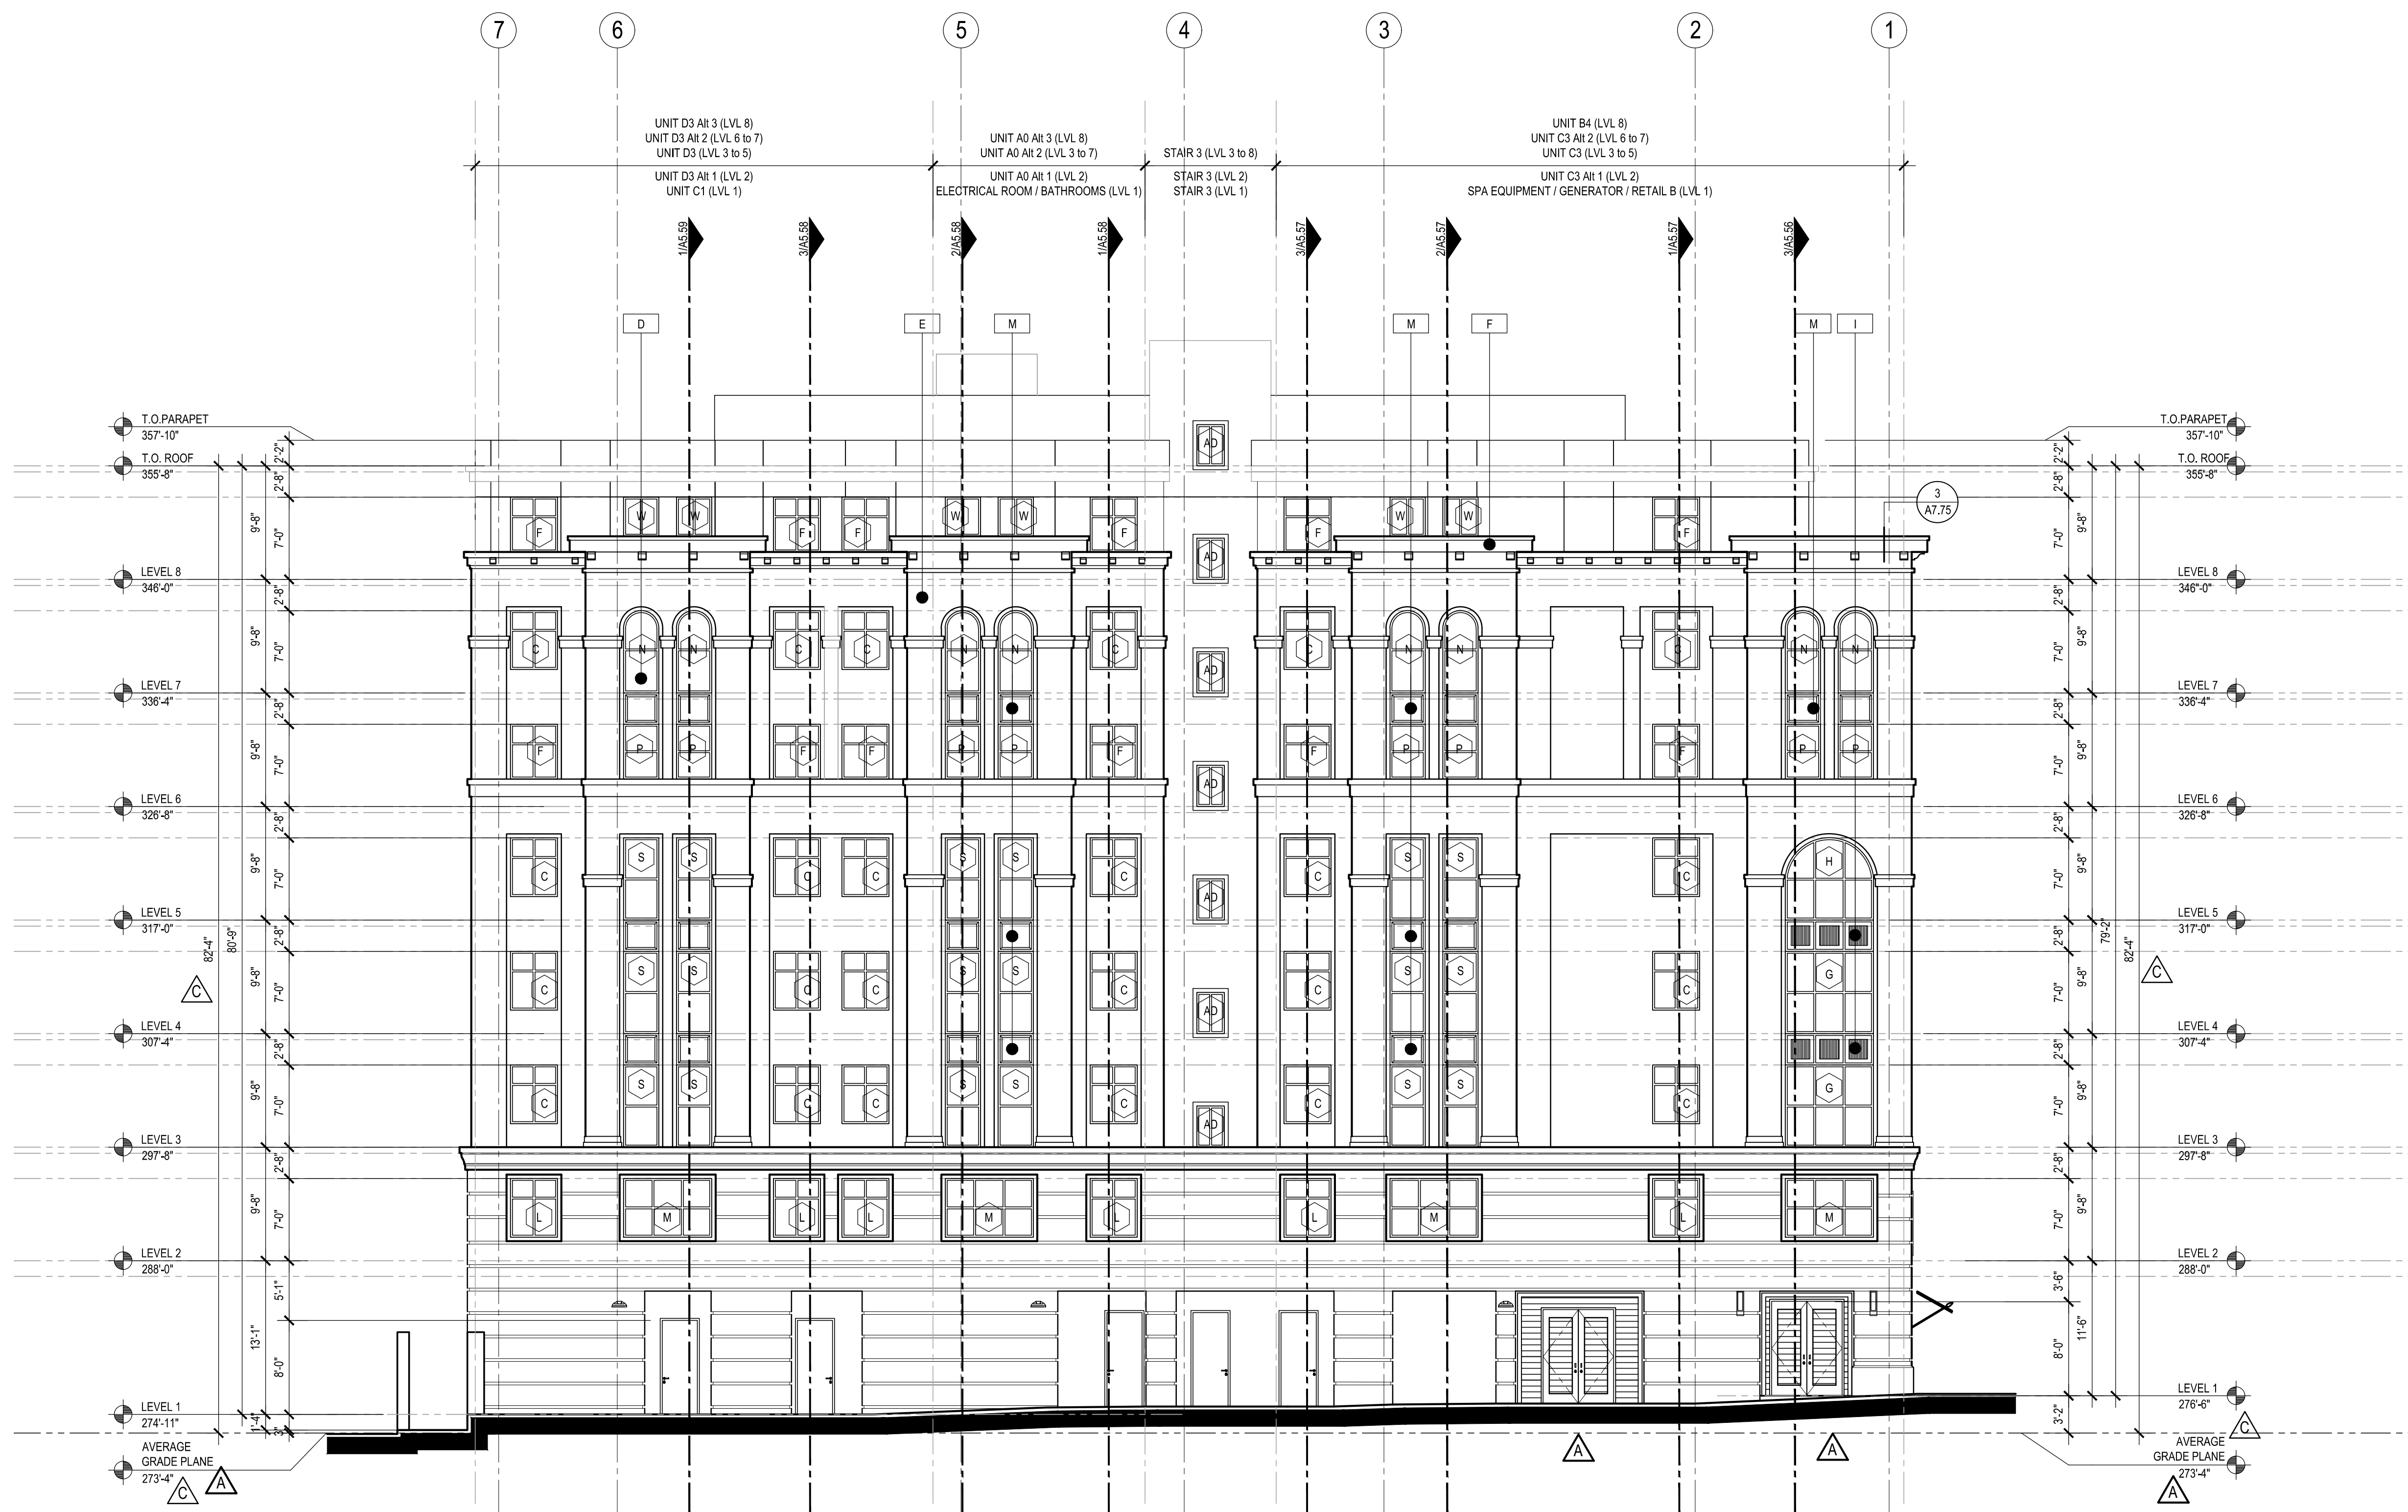

1 EAST ELEVATION
SCALE: 1/8" = 1'-0"

MATERIAL AND COLOR KEYNOTES

- A - STANDING SEAM COPPER METAL AWNING
- B - GREEN GRANITE BASE
- C - EXISTING FRED TURNER BUILDING RESIDENTIAL ENTRY
- D - VINYL CLAD WINDOWS
- E - PLASTER WITH SAND FINISH
- F - DECORATIVE CORNICE
- G - METAL RAILING
- H - COMPOSITE PANELS
- I - COPPER PANELS
- J - CORNICE BAND
- K - CONCRETE PLANTER WITH GLASS PANEL RAILING
- L - METAL PANELS
- M -

Designed by:	GH	
Drawn by:	GH	
Architect of Record:	Vince Chupka	
Date Plotted:		
Issue for Pricing / Bidding:	00/00/00	
Issue for Permit Application:	00/00/00	
Issue for Construction:	00/00/00	
Revisions:		
#	DATE	COMMENTS
1	10/16/2018	1 PLAN CHECK COMMENTS
2	12/05/2018	2 PLAN CHECK COMMENTS
3	01/14/2019	3 PLAN CHECK COMMENTS

© 2019 by Humphreys & Partners Architects, L.P.
All Rights Reserved
The architectural works depicted herein are the sole property of Humphreys & Partners Architects, L.P. and may not be constructed or used without its express written permission. No permission to modify or reproduce any of the architectural works, including without limitation the construction of any building, is expressed or should be implied from delivery of preliminary drawings or unsealed construction drawings. Permission to construct the building depicted in sealed construction drawings is expressly conditioned on the full and timely payment of all fees otherwise due Humphreys & Partners Architects, L.P. and, in the absence of any written agreement to the contrary, is limited to a one-time use on the site indicated on these plans.

THE STANDARD
BERKELEY, CA
LANDMARK CONSTRUCTION, LLC

HUMPHREYS & PARTNERS
ARCHITECTS, L.P.

5339 ALPHA ROAD - SUITE 300 - DALLAS, TEXAS 75240
(972) 701-9639 / (972) 701-9639 FAX
DALLAS · CHICAGO · NEW ORLEANS · NEW YORK · NEWPORT BEACH · ORLANDO
SAN RAMON · SCOTTSDALE · EDMONTON · TORONTO · MONTEVIDEO
www.humphreys.com




SHEET CONTENTS:

EAST ELEVATION

SHEET NO.

A5.04

15434

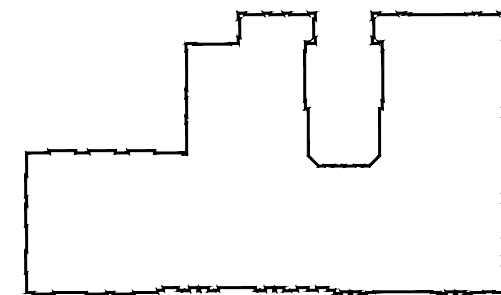

KEY PLAN


← EAST



NORTH

FIRST CITY SUBMITTAL 02-01-19

FILE: M15434.LandmarkStandard04_CD500_ELEV_SECTIONS\A5-1-A5.05-ELEVATIONS.dwg
USER: ghilgus DATE/TIME: Feb 01, 2019 - 1:50pm
SCALE: 1/8" = 1'-0"

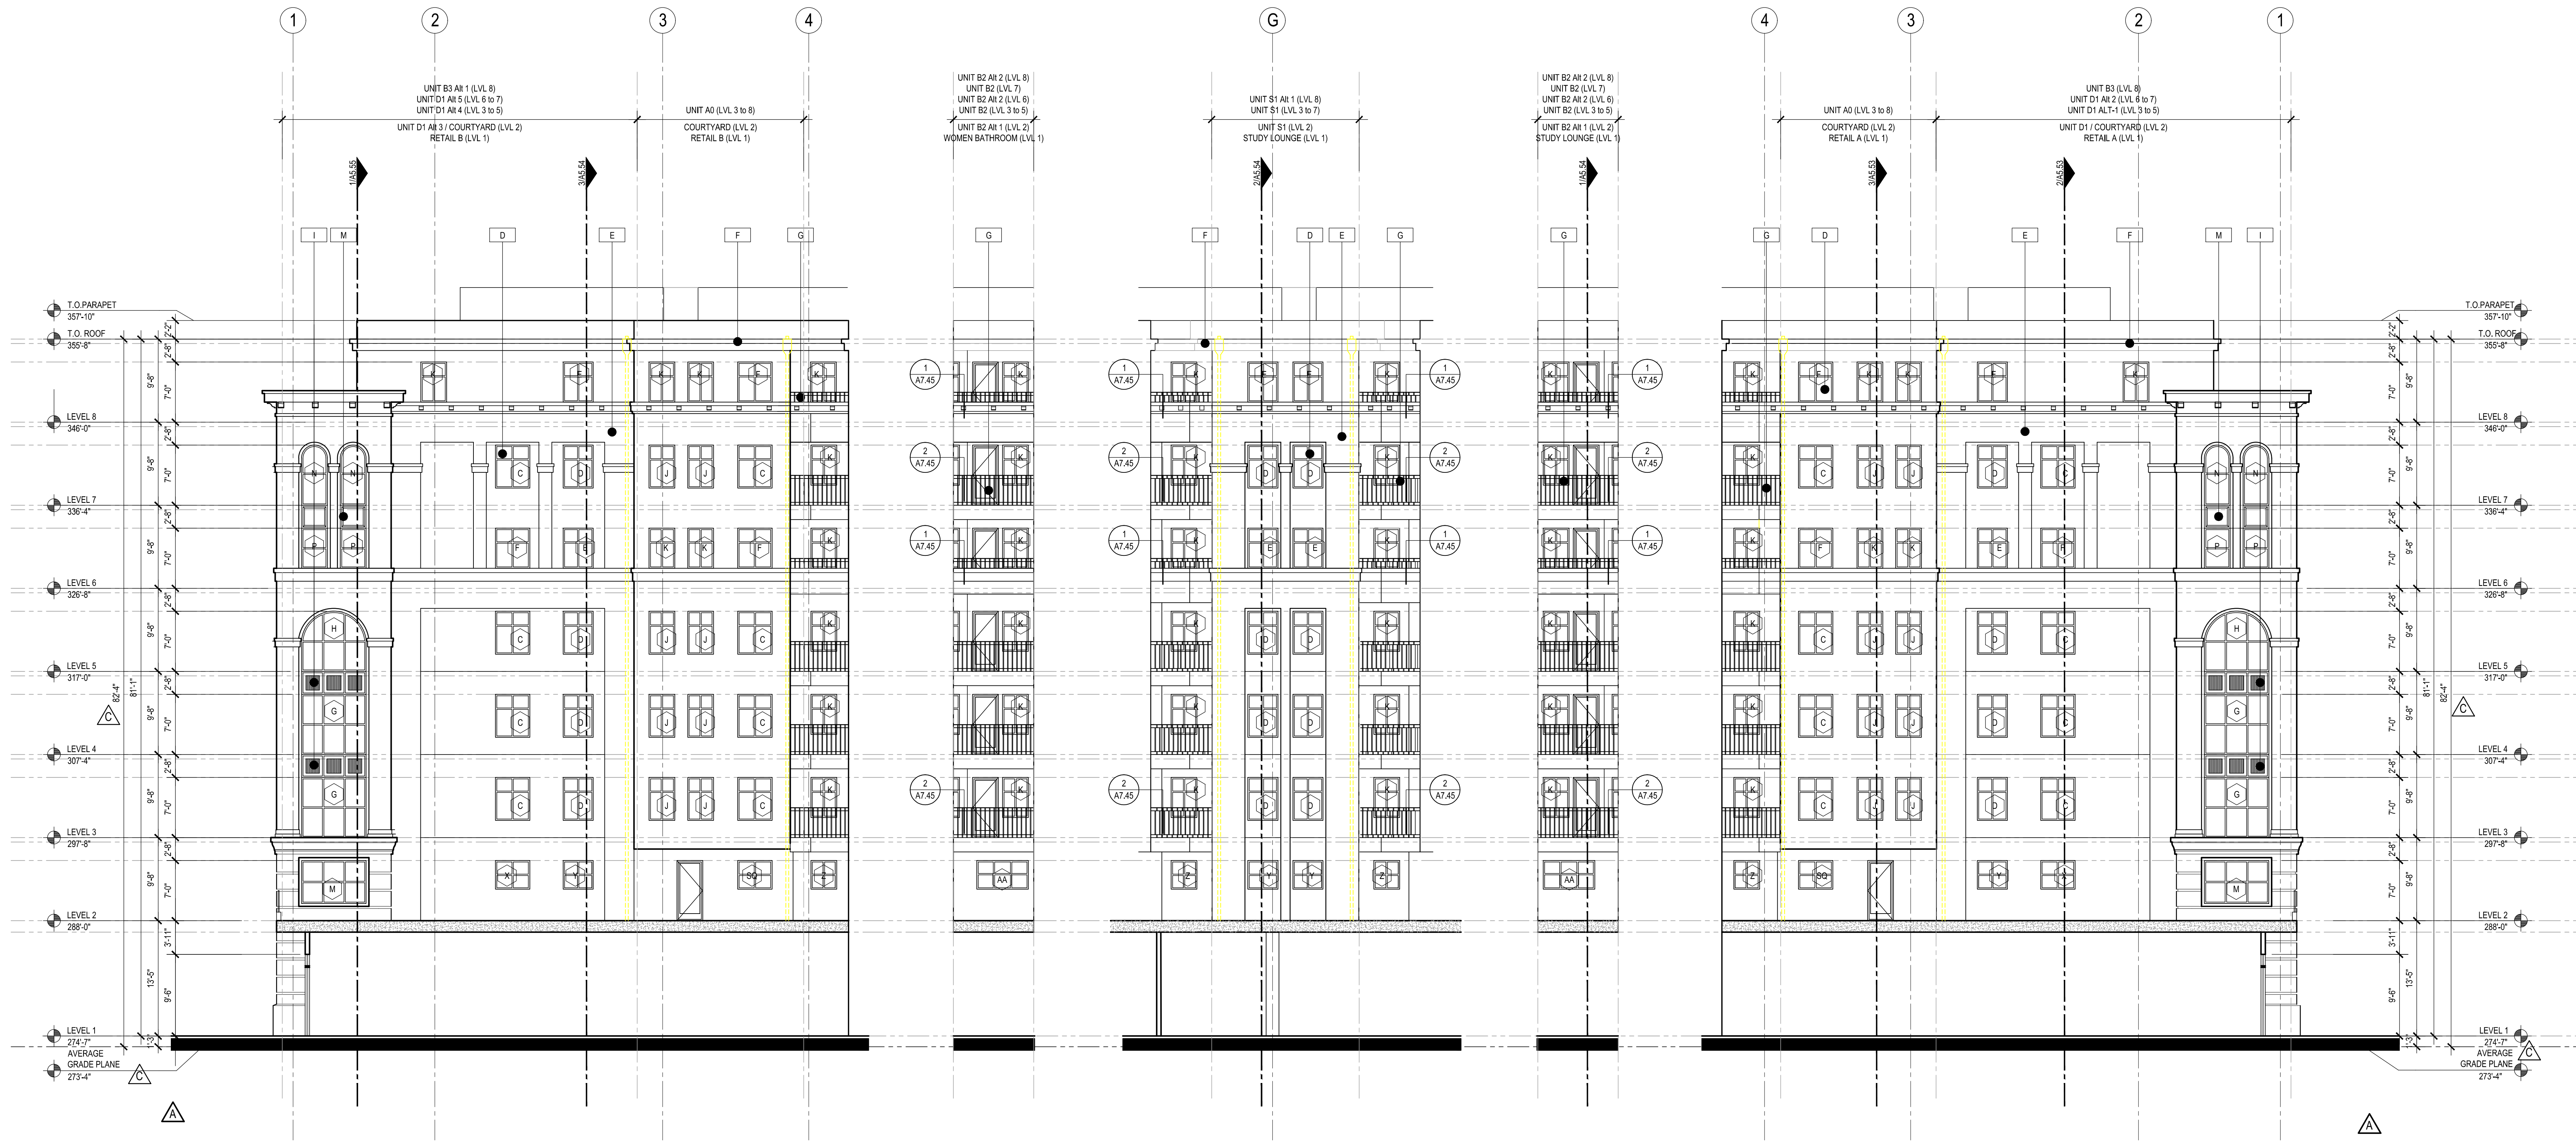

3 COURTYARD ELEVATION
SCALE: 1/8" = 1'-0"

2 COURTYARD ELEVATION
SCALE: 1/8" = 1'-0"

1 COURTYARD ELEVATION
SCALE: 1/8" = 1'-0"

KEY PLAN



MATERIAL AND COLOR KEYNOTES

- A - STANDING SEAM COPPER METAL AWNING
- B - GREEN GRANITE BASE
- C - EXISTING FRED TURNER BUILDING RESIDENTIAL ENTRY
- D - VINYL CLAD WINDOWS
- E - PLASTER WITH SAND FINISH
- F - DECORATIVE CORNICE
- G - METAL RAILING
- H - COMPOSITE PANELS
- I - COPPER PANELS
- J - CORNICE BAND
- K - CONCRETE PLANTER WITH GLASS PANEL RAILING
- L - METAL PANELS

Designed by:	GH	
Drawn by:	GH	
Architect of Record:	Vince Chupka	
Date Plotted:		
Issue for Pricing / Bidding:	00/00/00	
Issue for Permit Application:	00/00/00	
Issue for Construction:	00/00/00	
Revisions:		
#	DATE	COMMENTS
	10/16/2018	1 PLAN CHECK COMMENTS
	12/05/2018	2 PLAN CHECK COMMENTS
	01/14/2019	3 PLAN CHECK COMMENTS

© 2019 by Humphreys & Partners Architects, L.P.
All Rights Reserved
The architectural works depicted herein are the sole property of Humphreys & Partners Architects, L.P. and may not be constructed or used without its express written permission. No permission to modify or reproduce any of the architectural works, including without limitation the construction of any building, is expressed or should be implied from delivery of preliminary drawings or unsealed construction drawings. Permission to construct the building depicted in sealed construction drawings is expressly conditioned on the full and timely payment of all fees otherwise due Humphreys & Partners Architects, L.P. and, in the absence of any written agreement to the contrary, is limited to a one-time use on the site indicated on these plans.

THE STANDARD
BERKELEY, CA
LANDMARK CONSTRUCTION, LLC

HUMPHREYS & PARTNERS
ARCHITECTS, L.P.

5339 ALPHA ROAD - SUITE 300 - DALLAS, TEXAS 75240
(972) 701-9639 / (972) 701-9639 FAX
DALLAS, CHICAGO, NEW ORLEANS, NEW YORK, NEWPORT BEACH, OCEANO
SAN RAMON, SCOTTSDALE, EDMONTON, TORONTO, MONTREAL
www.humphreys.com



SHEET CONTENTS:
COURTYARD
ELEVATIONS

SHEET NO.

A5.05

15434

FIRST CITY SUBMITTAL 02-01-19